


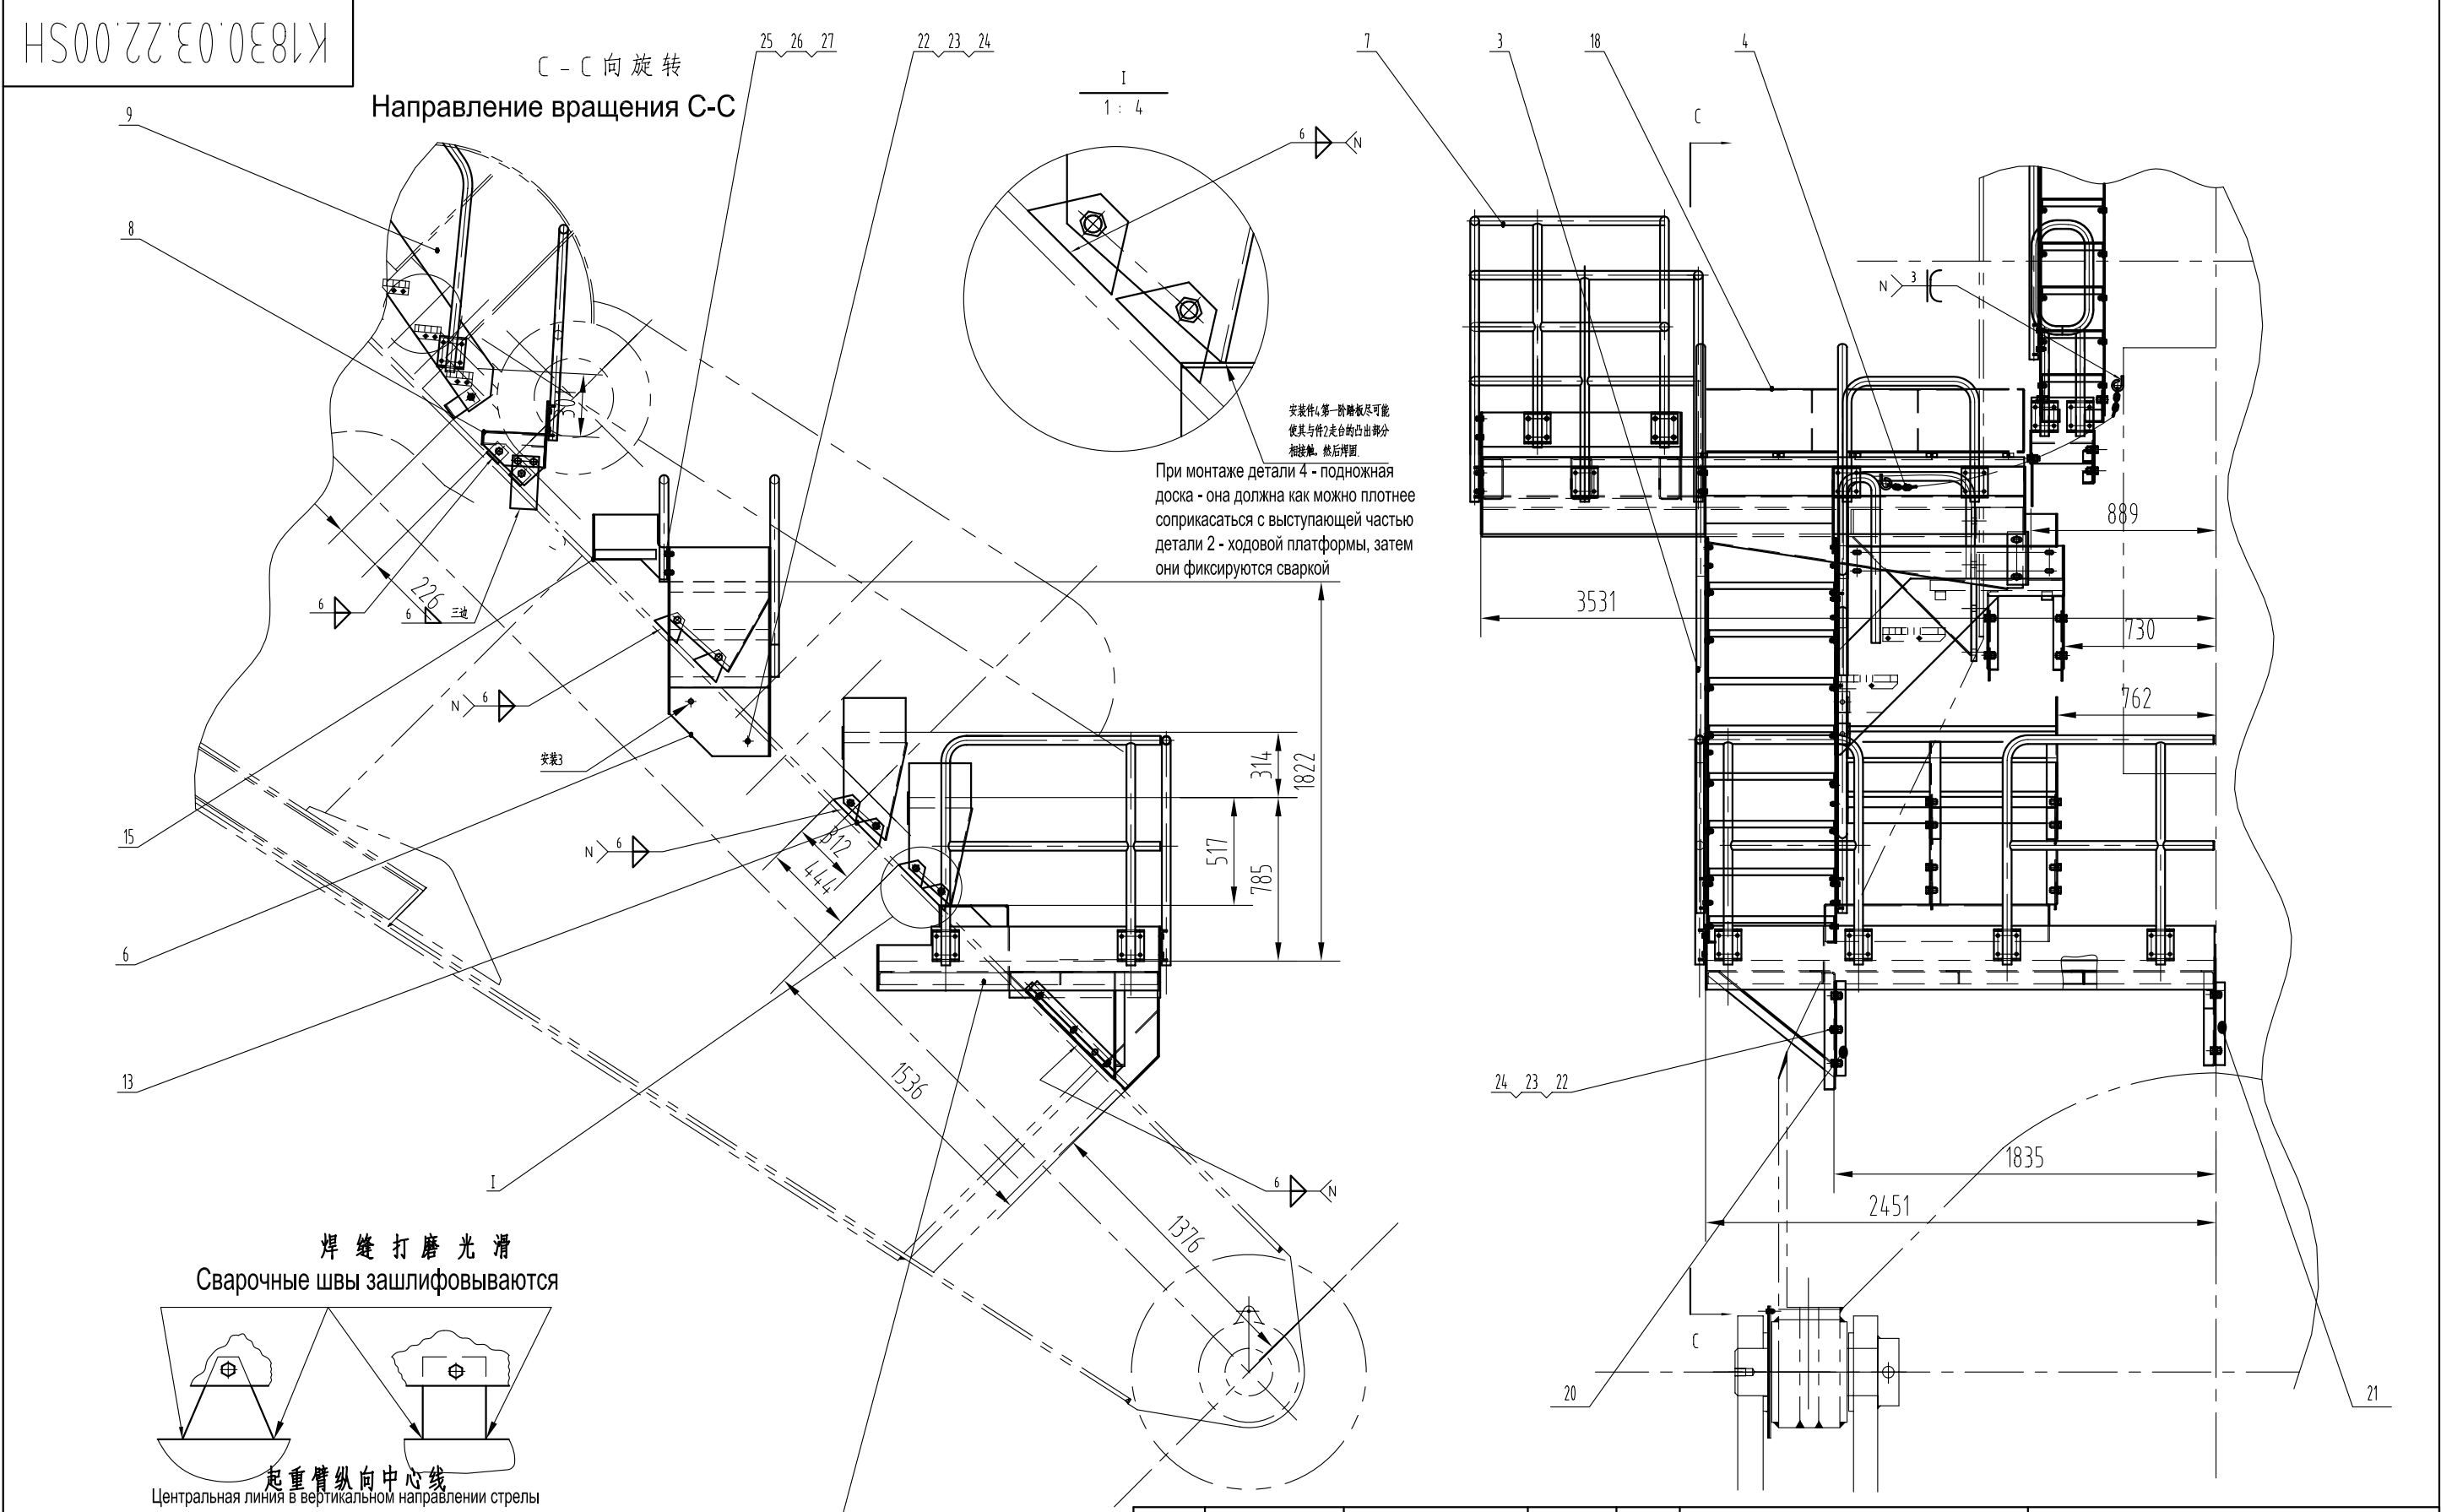

Примечания: фиксирующие планки платформы с лестницей, а также уголовая сталь должны привариваться вдоль центральной линии в вертикальном направлении стрелы, не допустима сварка в горизонтальном направлении. После сварки сварочные корни шлифуются.

说明：梯子走台等的固定板及角钢应沿起重臂纵向中心线施焊，不得沿横向施焊，并在焊后打磨焊脚。

Отметка	Кол-во	Номер документа	Подпись	Дата
Проектировщик		Технологическая проверка		
Контроль				
Главный проектировщик				
Проверил		Проверка стандартов		
Директор института		Дата		

起重臂走台
Проходная платформа
стрелы

通用技术条件
ОБЩЕПРИНЯТЫЕ ТЕХНИЧЕСКИЕ УСЛОВИЯ
JB/T 5000

K1830.03.22.00SH

重量 Вес 比例 Масштаб 1:30

共5张 Всего5 листа 第3张 Лист3



太重技术中心
Технический центр тяжелой
техники, Тайюань