
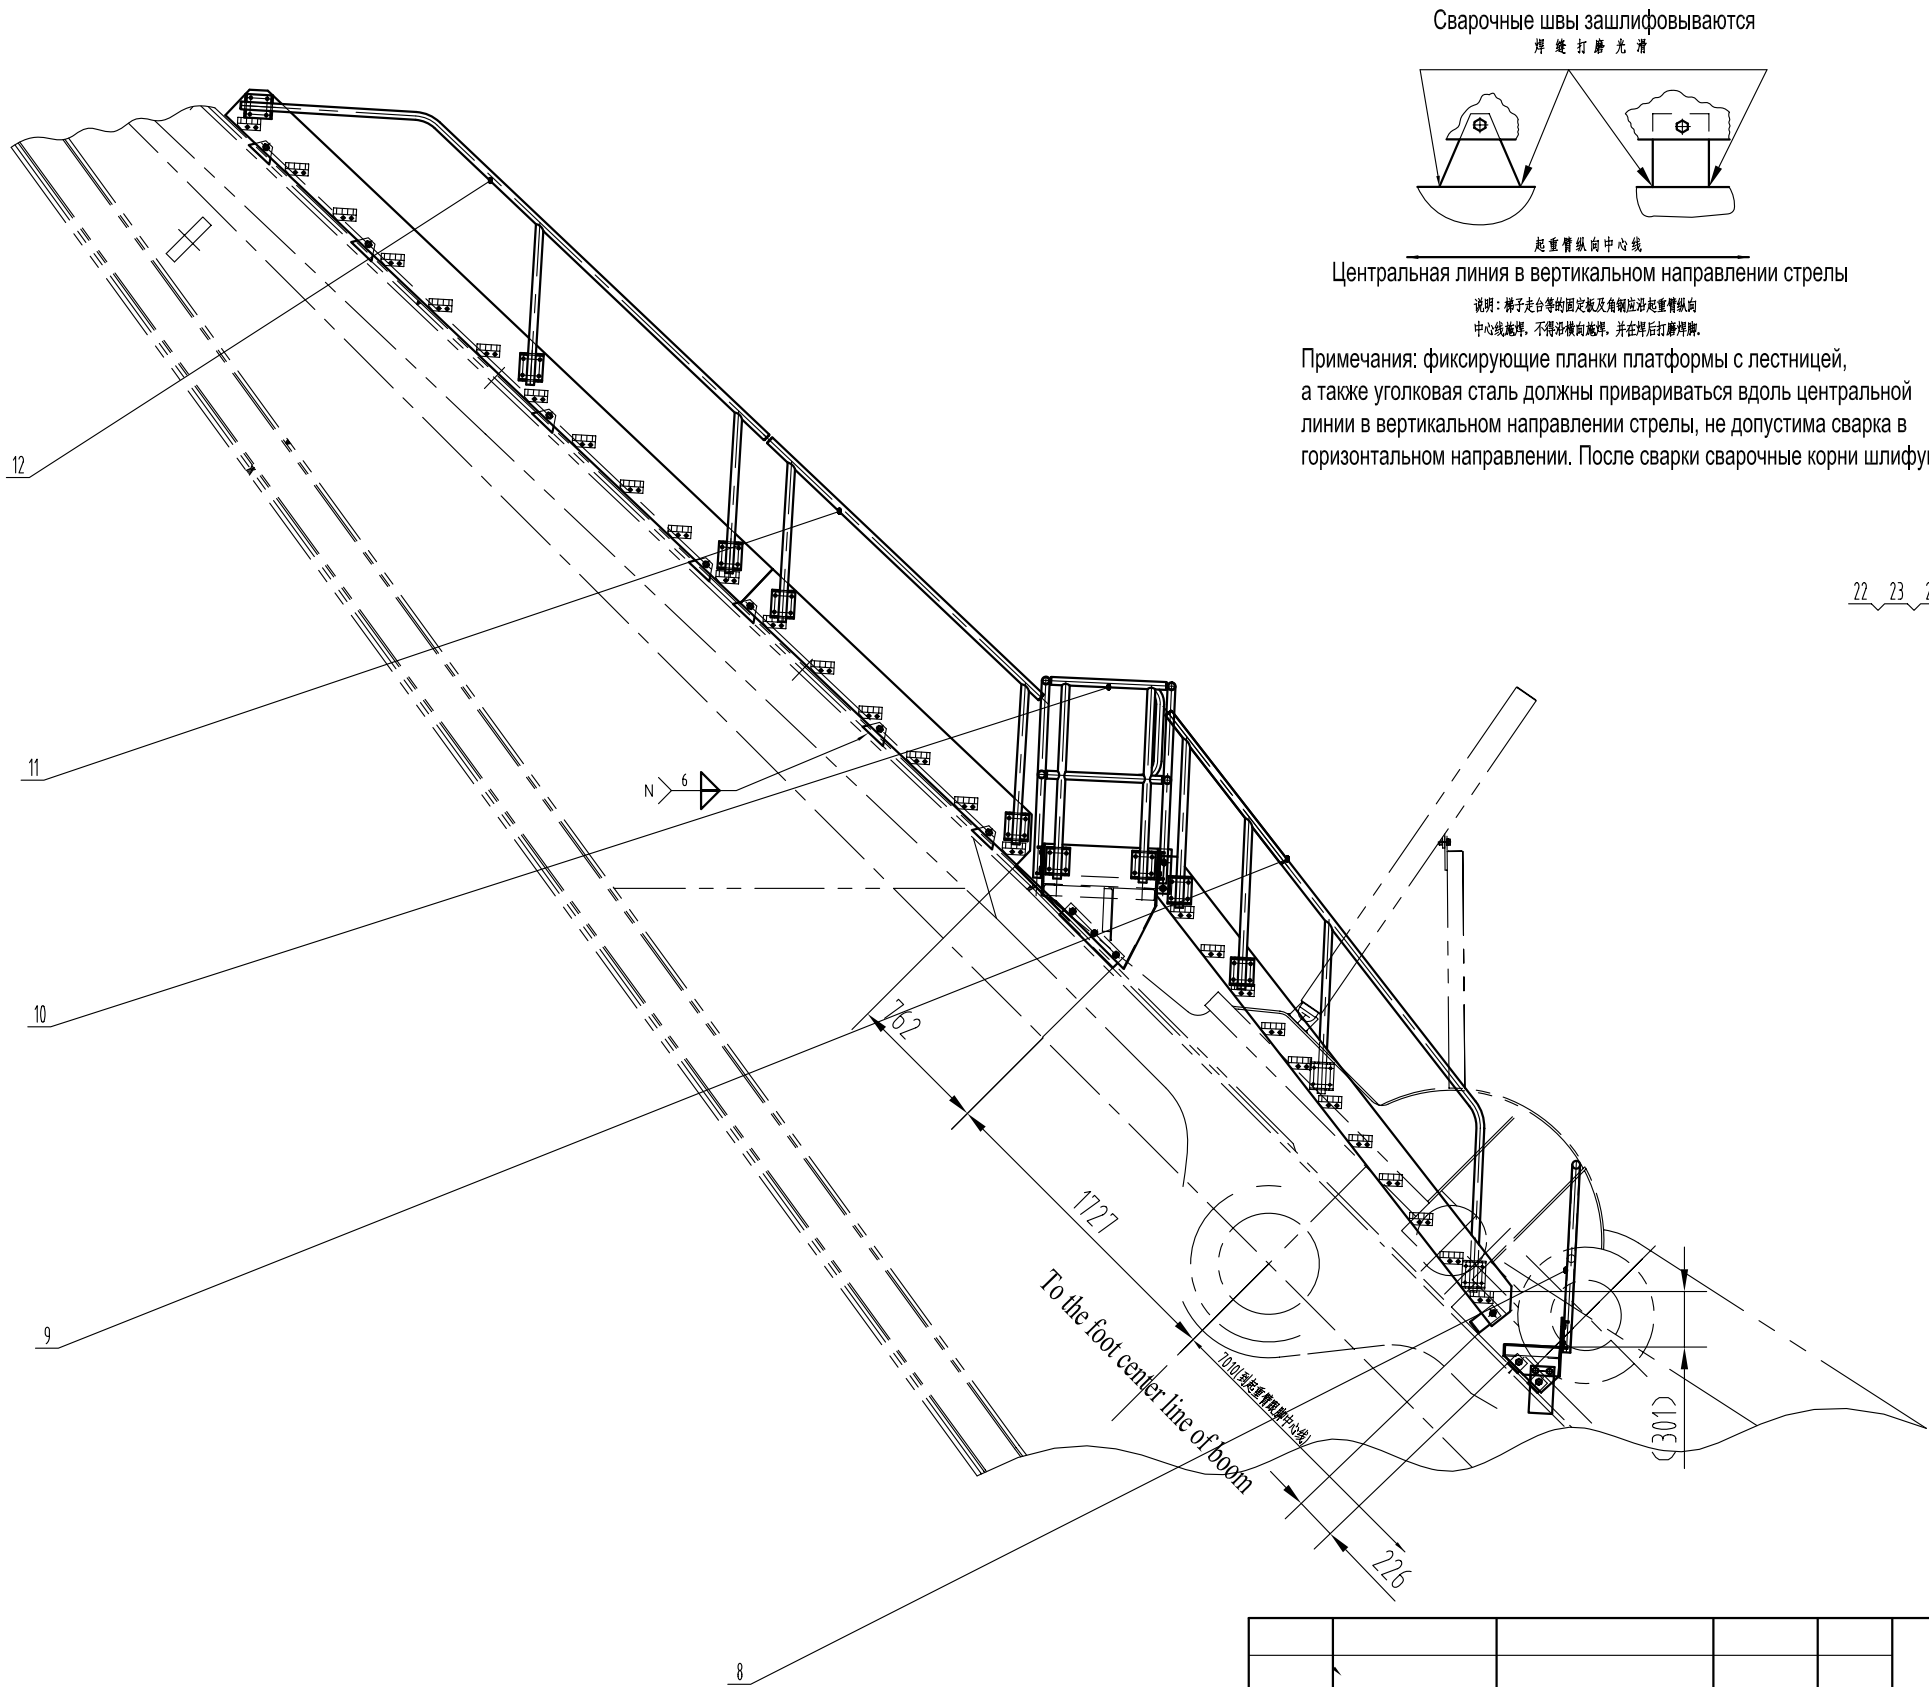


Центральная линия в вертикальном направлении стрелы

说明：梯子走台的固定板及角钢应沿起重臂纵向中心线施焊，不得沿横向施焊，并在焊后打磨焊脚。

Примечания: фиксирующие планки платформы с лестницей, а также уголовая сталь должны привариваться вдоль центральной линии в вертикальном направлении стрелы, не допустима сварка в горизонтальном направлении. После сварки сварочные корни шлифуются.

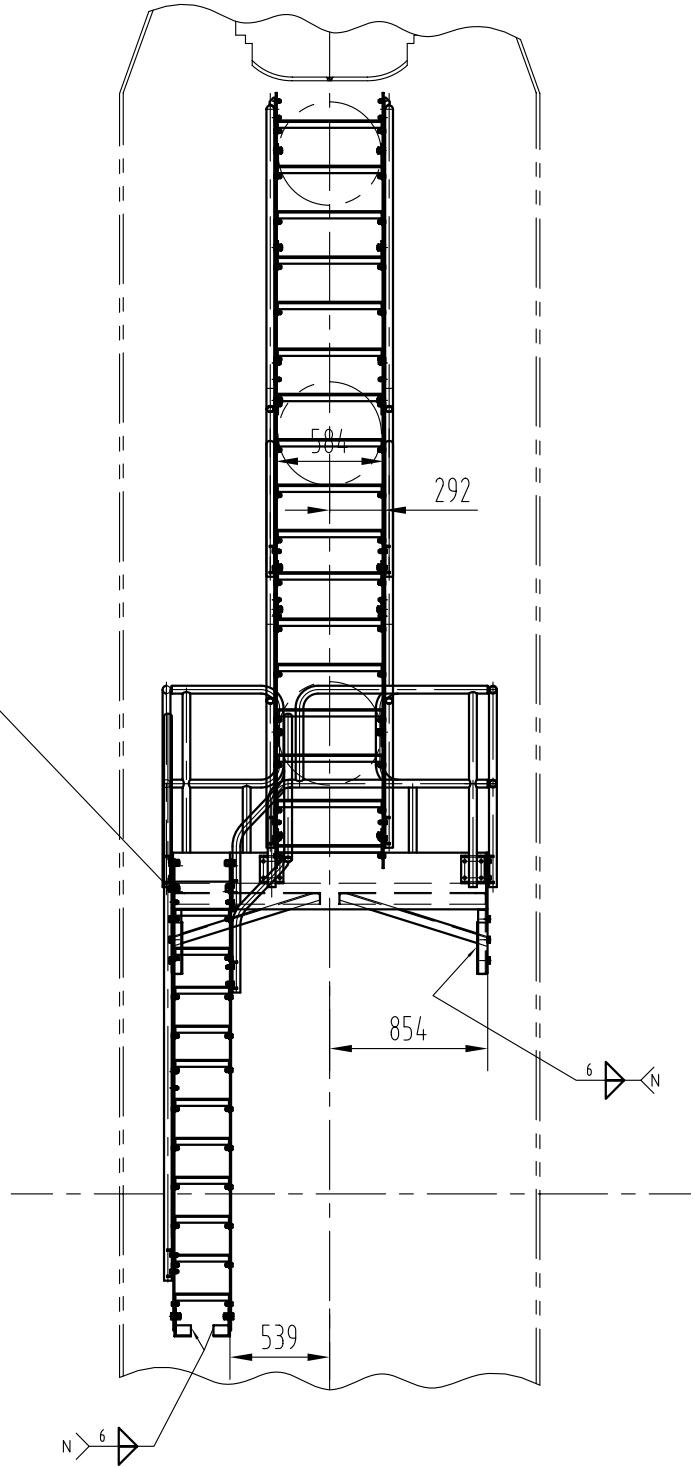

					起重臂走台 Proходная платформа стрелы	K1830.03.22.00SH			
Отметка	Кол-во	Номер документа	Подпись	Дата		重量 Вес		比例 Масштаб	1:4.0
Прокетировщик		Технологическая проверка			通用技术条件 ОБЩЕПРИНЯТЫЕ ТЕХНИЧЕСКИЕ УСЛОВИЯ JB/T 5000	共5张	Всего5 листа	第4张	Лист4
Контроль						 太重技术中心 Технический центр тяжелой техники, Тайюань			
Главный проектировщик		Проверка стандартов							
Проверил		Дата							
Директор института									