
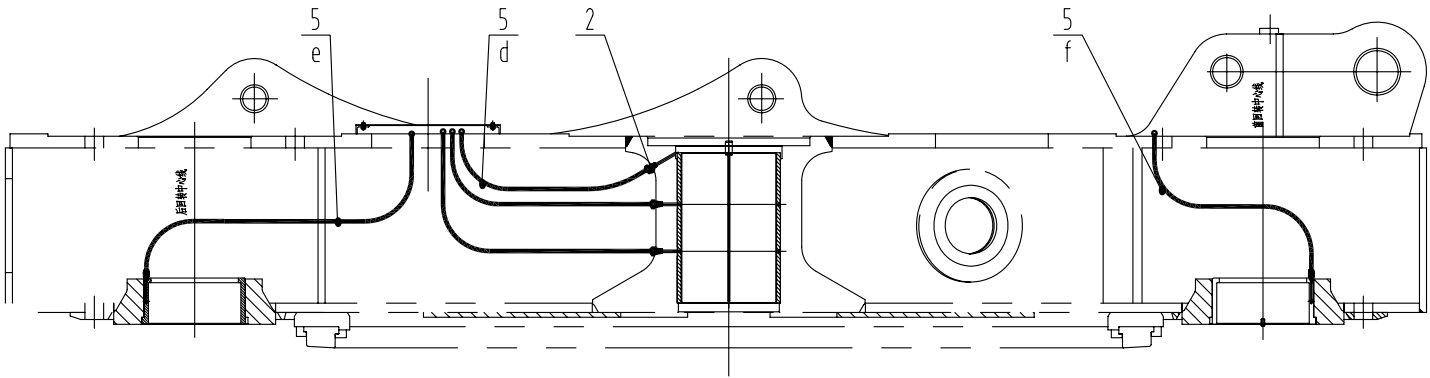
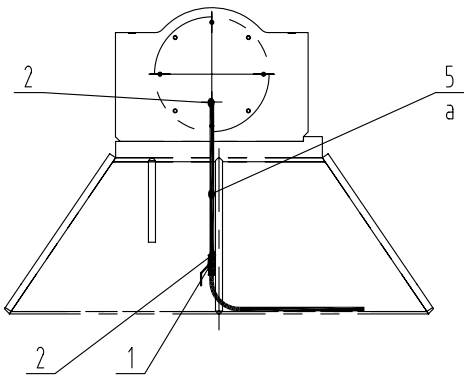


HS00'E0'06'8E81K

标记	处数	文件号	签字	日期

A向局部

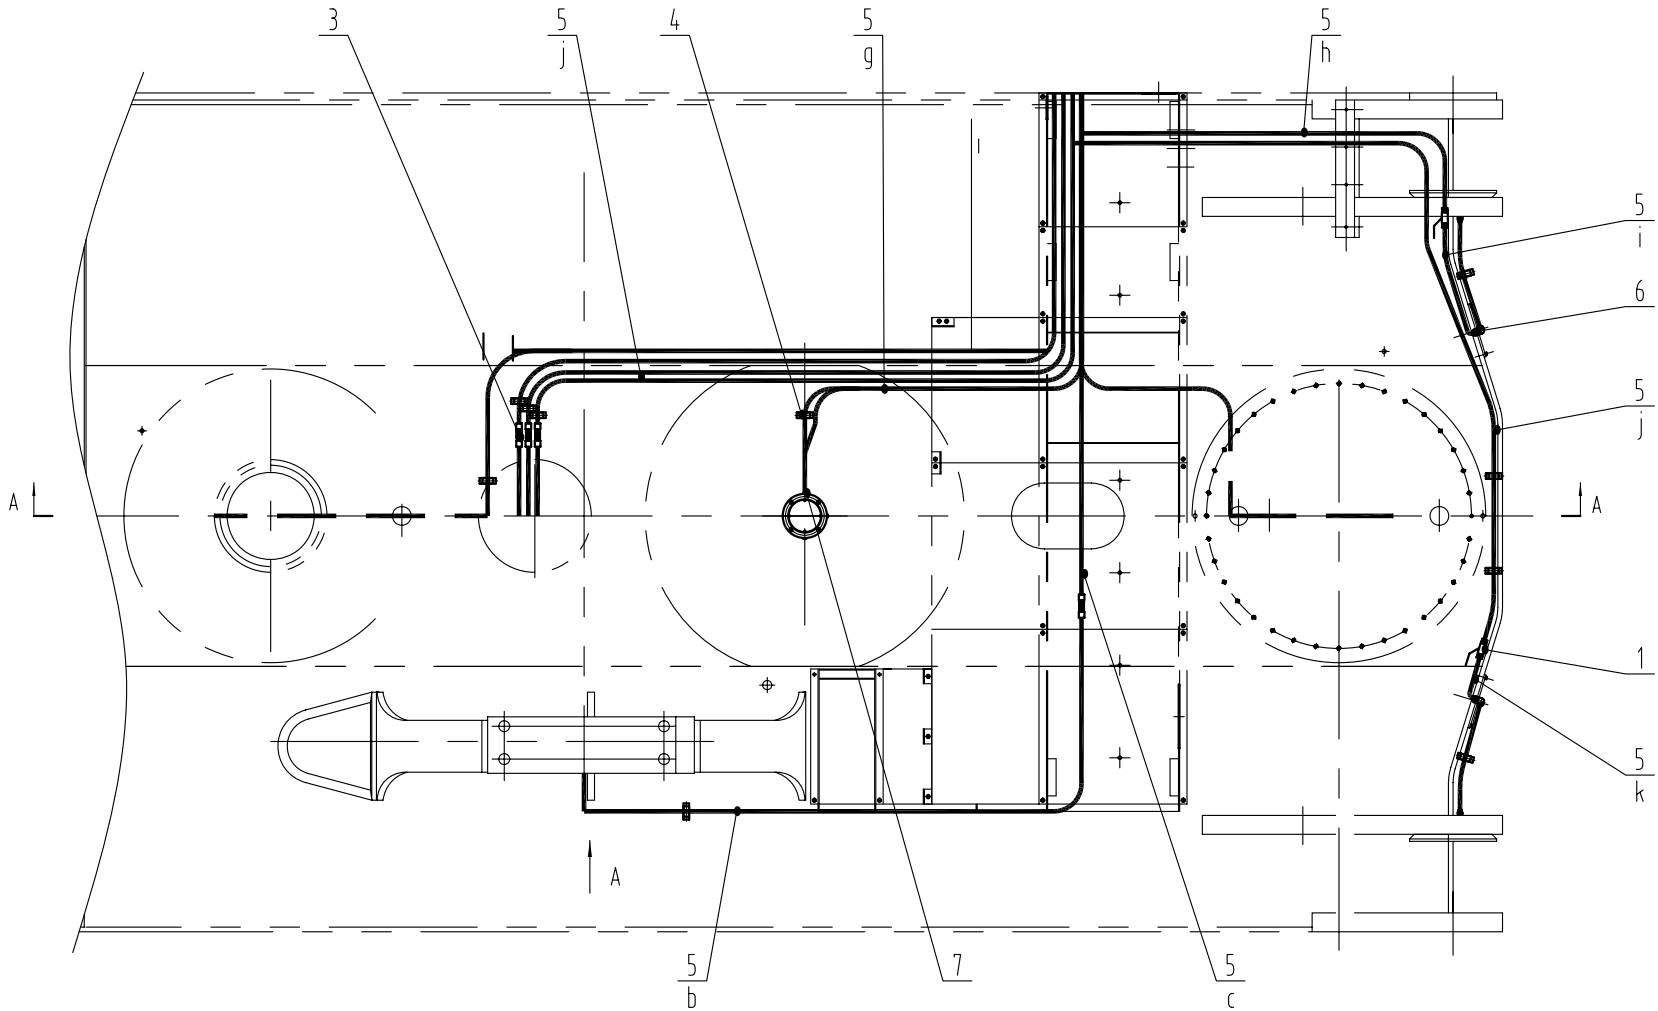

7	10MJ-6MT	Конец прямого штуцера	3	
6	10MJ-10BKHD-LN	Конец прямого штуцера	2	
5	K1838.90.03.01	Устройство смазочного шланга	1	
4	DIN3015	Монтажная рейка зажима трубы TLPG1-325	26	
3	10MJ-10MJ	Конец прямого штуцера	8	
2	10MJ-6MT	Конец прямого штуцера	14	
1	KHB-G3/8-PN500	Сферический клапан, высокого давления	3	

7	10MJ-6MT	端直连接头	3	
6	10MJ-10BKHD-LN	隔板接头	2	
5	K1838.90.03.01	润滑胶管总成	1	
4	DIN3015	管夹TLP G1-325	26	
3	10MJ-10MJ	直连接头	8	
2	10MJ-6MT	端直连接头	14	
1	KHB-G3/8-PN500	高压球阀	3	
序号	代 号	名 称	数量	备 注

P001003836-A				平台集中润滑布置		K1838.90.03.00SH			
设 计	卢安卿	工艺审查	袁运星	Кронштейн смазочного шланга					
校 核	吕晓林								
审 查	张玉姝	标准审查	白焱			重 量	64.5	比 例	1:40
主任设计		主管主任		通用技术条件 JB/T 5000		共 1 张		第 1 张	
所 长									
日 期	20161209								
						 太重技术中心			



太重技术中心