


HS00'80'EO'E081X

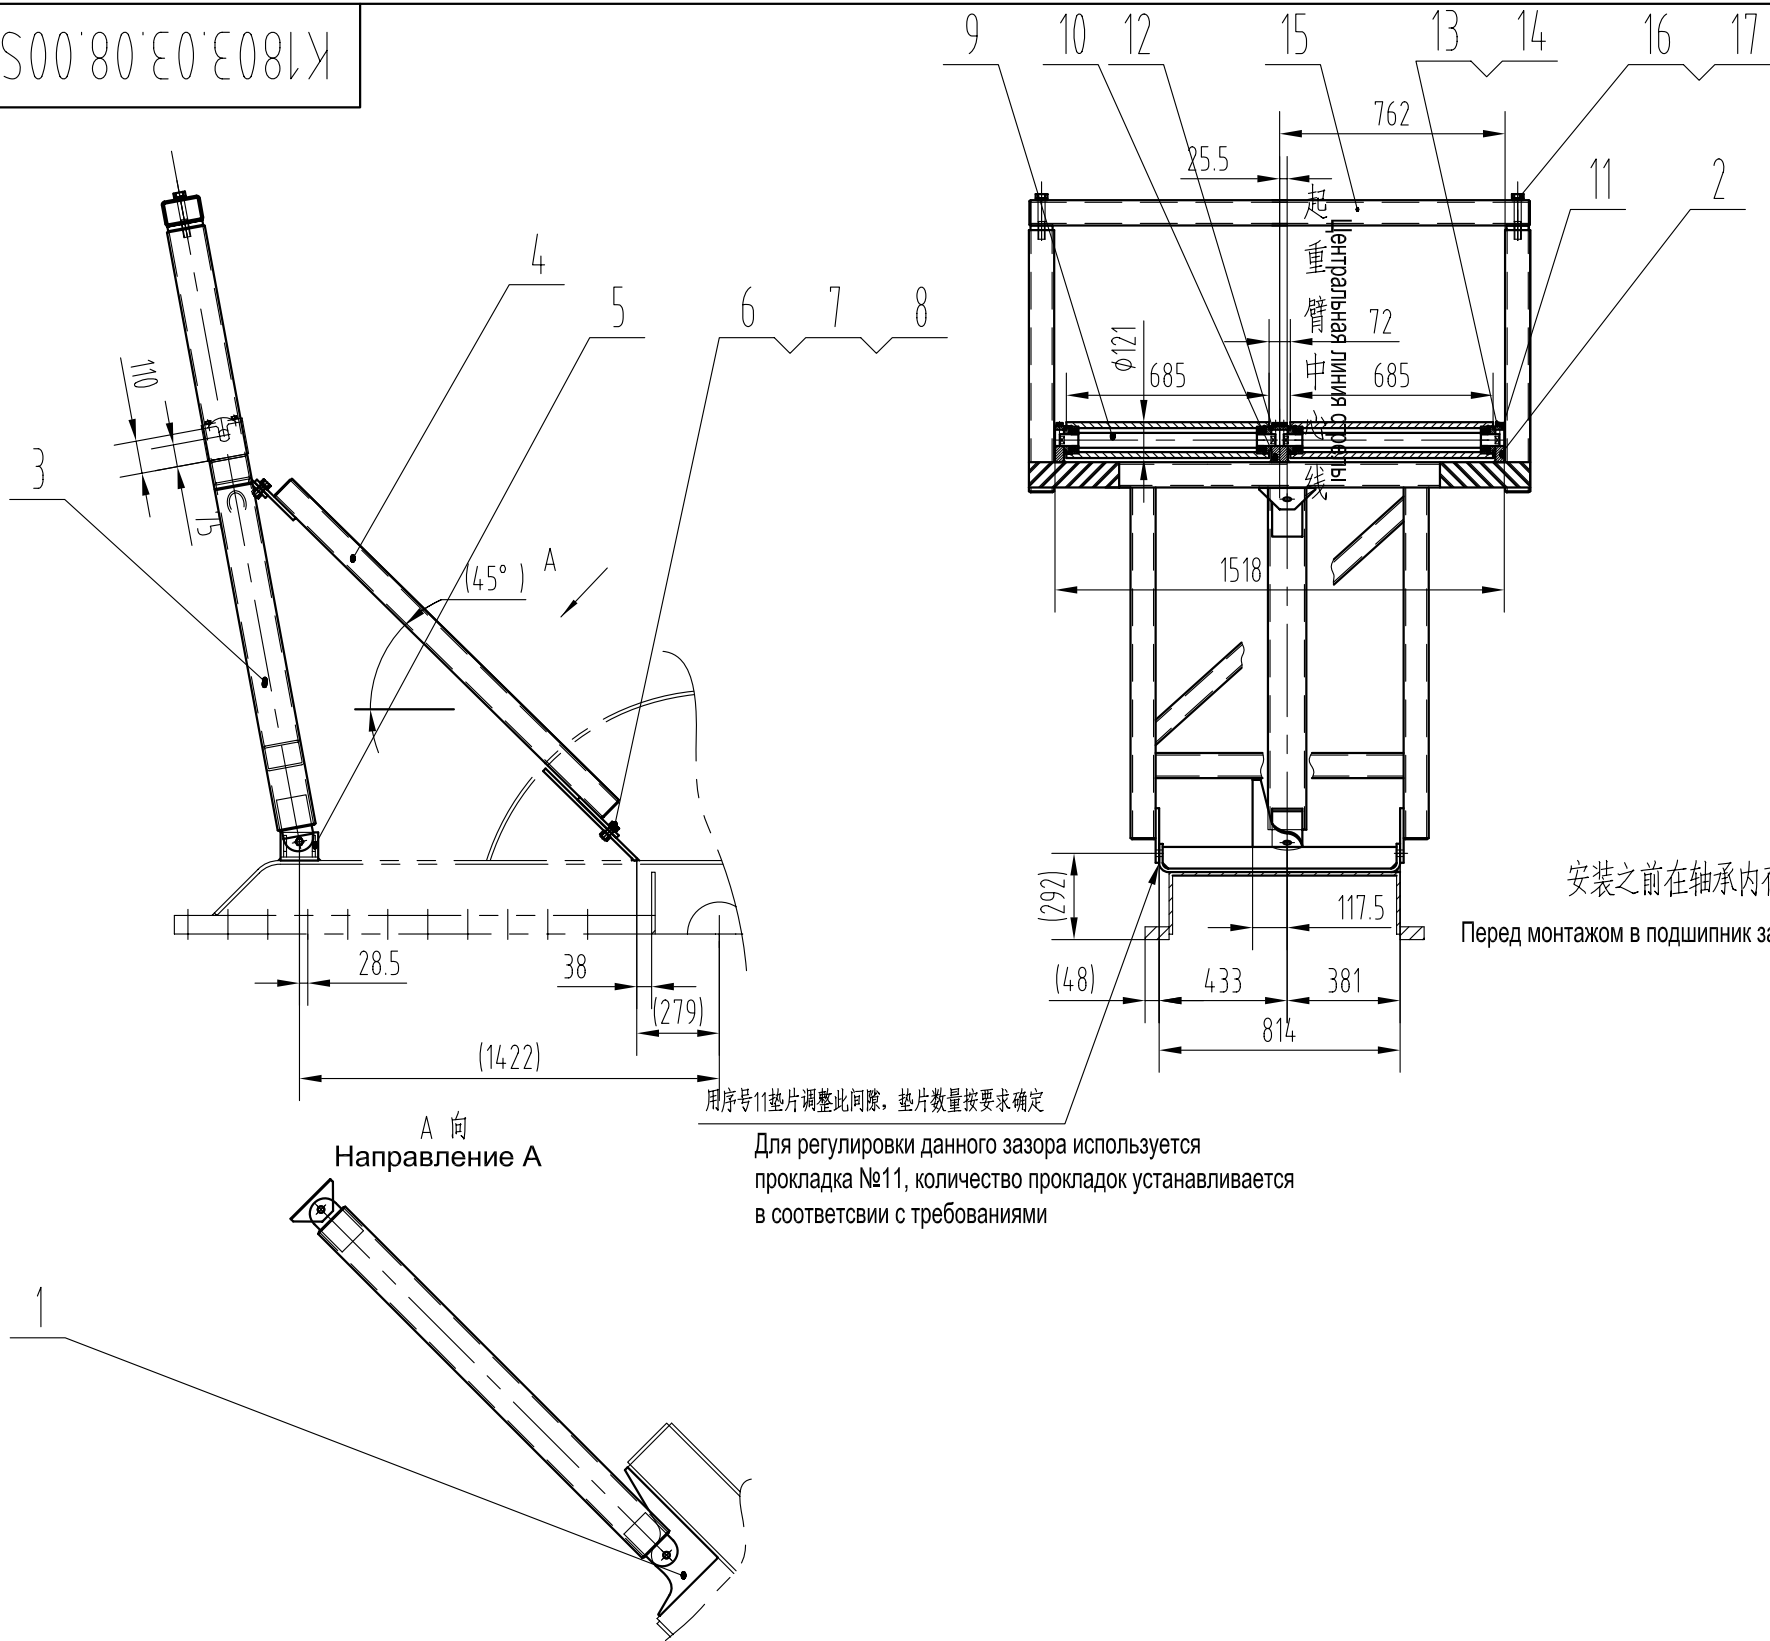

12	K1803.03.08.05	Прижимная крышка 2	1	
11	K1803.03.08.04	Прижимная крышка 1	2	
10	K1803.03.08.03	Прокладочная планка 2	1	
9	K1801.03.08.04.00	Роликоопора	2	
8	GB/T6170	Гайка M20	4	
7	GB/T93	Пружинящая шайба 20	4	
6	GB/T5783	Болт M20x50	4	
5	K1801.03.08.03.00	Кронштейн	1	
4	K1801.03.08.02.00	Тяговая штанга	1	
3	K1803.03.08.01.00	Опорные козлы	1	
2	K1803.03.08.02	Прокладочная планка	2	
1	K1801.03.08.01	-12x279x438	1	
№	Обозначение	Наименование	Кол-во	Примечания

17	GB/T93	垫圈24	2	
16	GB/T5782	螺栓M24X140	2	
15	K1803.03.08.05.00	活动杆	1	
14	GB/T93	垫圈12	8	
13	GB/T5783	螺栓M12X35	8	
12	K1803.03.08.05	压盖2	1	
11	K1803.03.08.04	压盖1	2	
10	K1803.03.08.03	垫板2	1	
9	K1801.03.08.04.00	托辊	2	
8	GB/T6170	螺母 M20	4	
7	GB/T93	弹簧垫圈 20	4	
6	GB/T5783	螺栓 M20x50	4	
5	K1801.03.08.03.00	托座	1	
4	K1801.03.08.02.00	拉杆	1	
3	K1803.03.08.01.00	托架	1	
2	K1803.03.08.02	垫板	2	
1	K1801.03.08.01	-12x279x438	1	
序号	代 号	名 称	数量	备 注

17	GB/T93	Прокладочное кольцо 24	2						
16	GB/T5782	Болт M24x140	2						
15	K1803.03.08.05.00	Подвижной рычаг	1						
14	GB/T93	Прокладочное кольцо 12	8						
13	GB/T5783	Болт M12x35	8						
№	Обозначение	Наименование	Кол-во	Примечания	Отметка	Кол-во	Номер документа	Подпись	Дата
					Проектировщик		Технологическая проверка		
					Контроль				
					Главный проектировщик				
					Проверил		Проверка стандартов		
					Директор института		Дата		

提升绳导向托架
Направляющие опорные
козлы подъемных тросов
通用技术条件
ОБЩЕПРИНЯТЫЕ ТЕХНИЧЕСКИЕ УСЛОВИЯ
JB/T 5000

K1803.03.08.00SH

重量 Вес
共1张 Всего1 листа
第1张 Лист1
比例Масштаб 1:25
太重技术中心
Технический центр тяжелой
техники, Тайюань