



K1830.03.22.00SH


A - A 向旋转
Направление вращения А-А

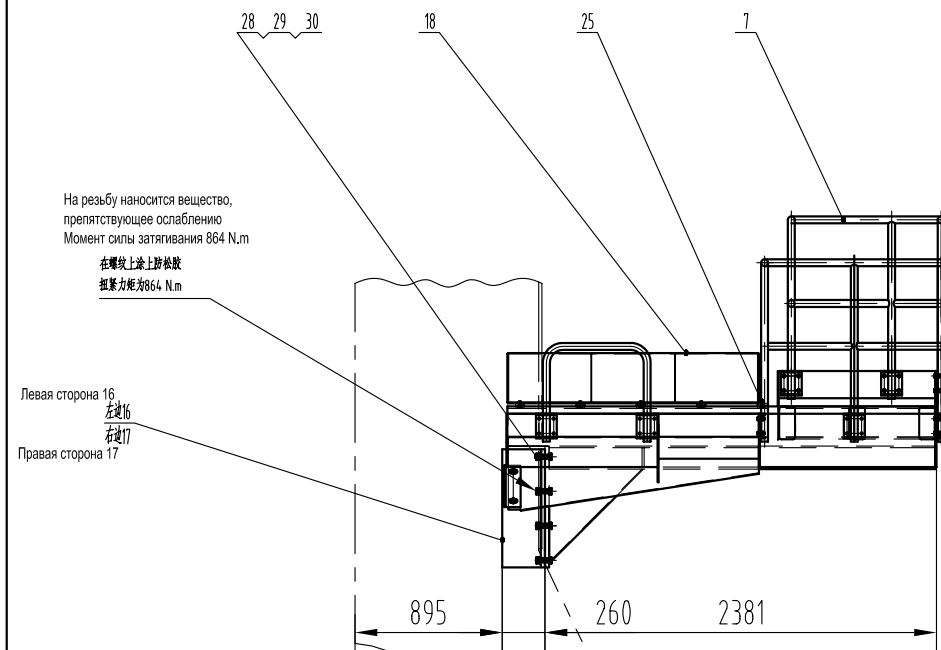

B - B 向旋转
Направление вращения В-В

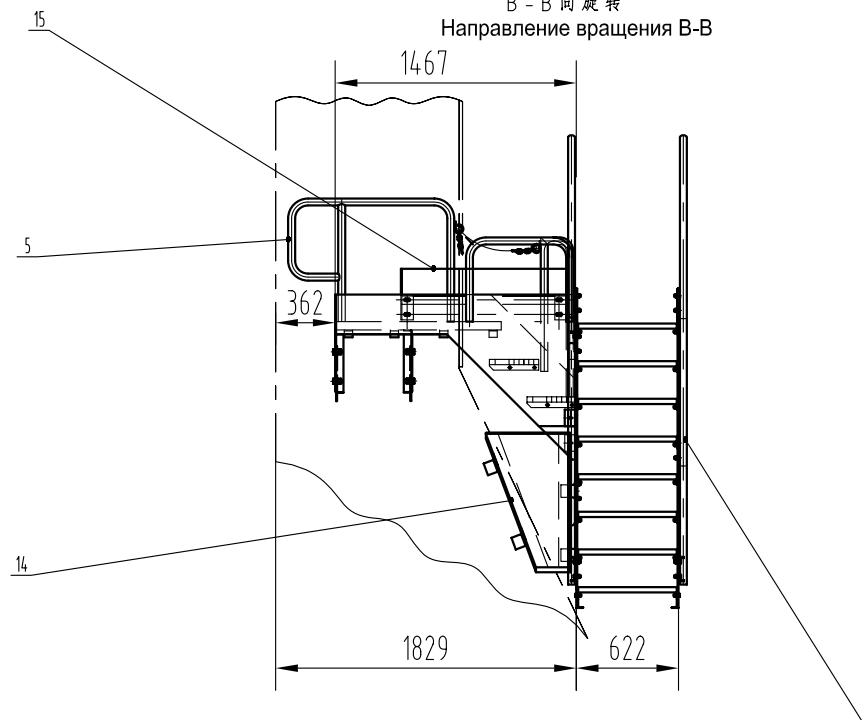

Сварочные швы зашлифовываются
焊缝打磨光滑

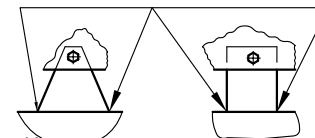


Центральная линия в вертикальном направлении стрелы

起重臂纵向中心线

说明：梯子走台等的固定板及角钢应沿起重臂纵向

中心线施焊,不得沿横向施焊,并在焊后打磨焊脚。

Примечания: фиксирующие планки платформы с лестницей, а также уголовая сталь должны привариваться вдоль центральной линии в вертикальном направлении стрелы, не допустима сварка в горизонтальном направлении. После сварки сварочные корни шлифуются.

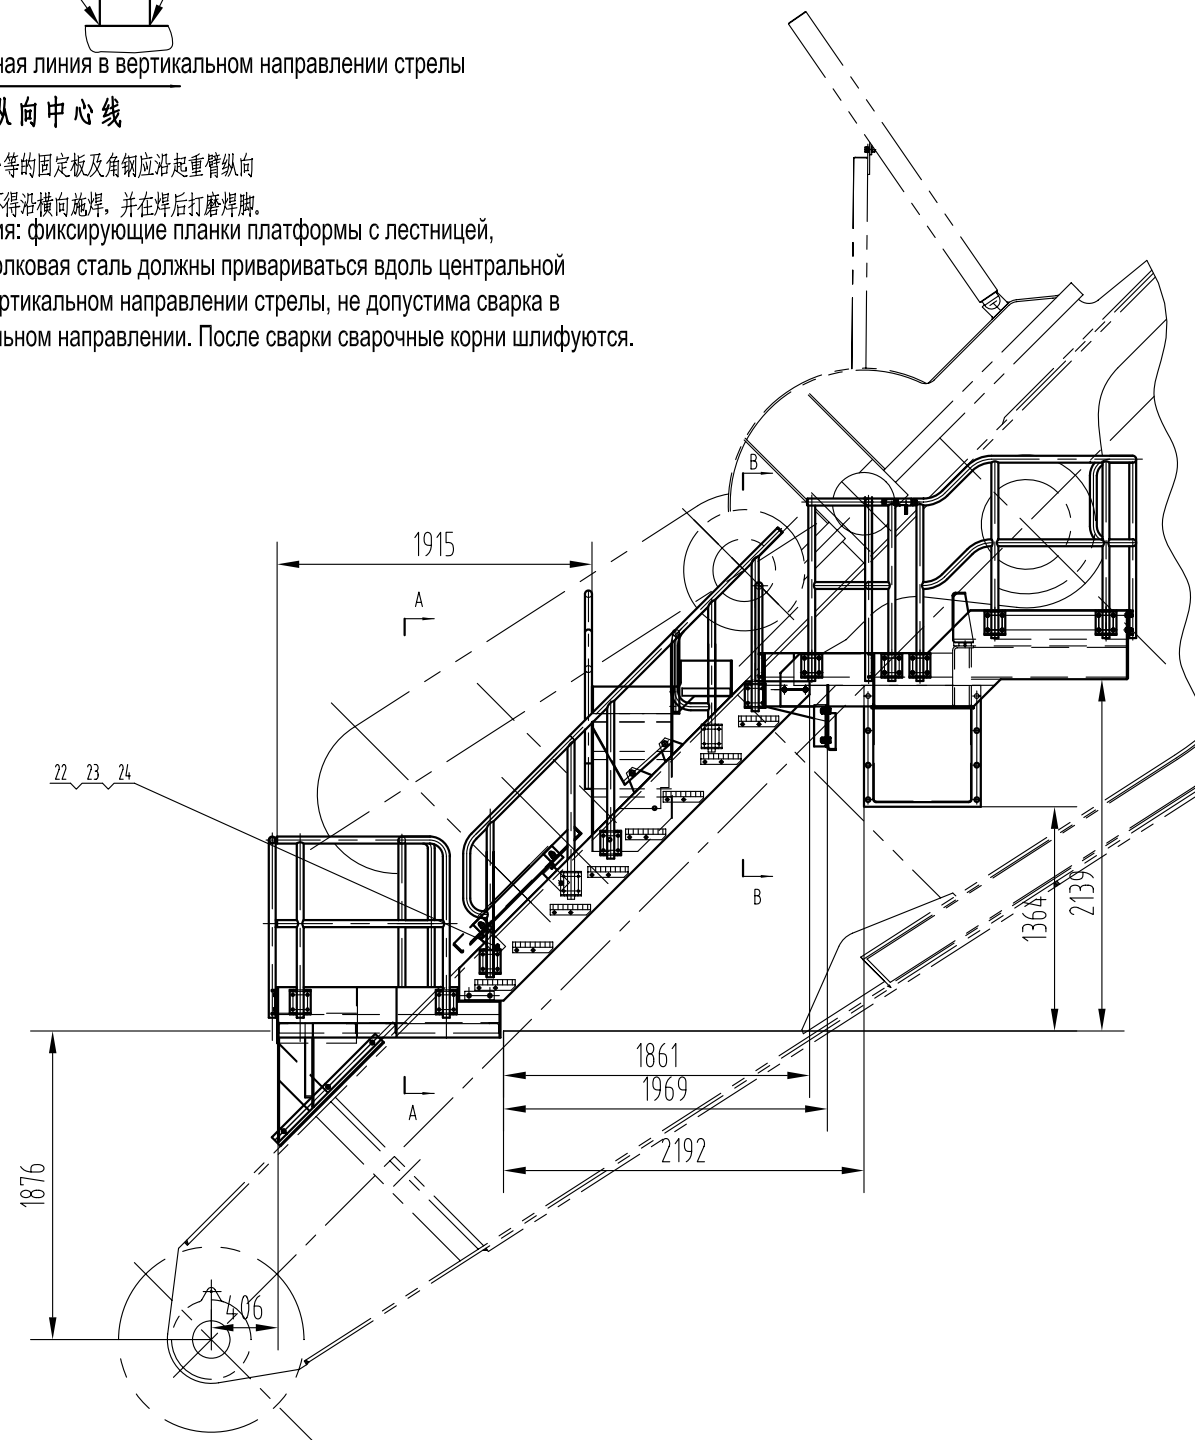

					起重臂走台 Проходная платформа стрелы	K1830.03.22.00SH			
Отметка	Кол-во	Номер документа	Подпись	Дата		重量 Вес		比例 Масштаб	1:40
Проектировщик		Технологическая проверка			通用技术条件 ОБЩЕПРИНЯТЫЕ ТЕХНИЧЕСКИЕ УСЛОВИЯ JB/T 5000	共5张		Всего листа	第2张 Лист2
Контроль						 大重技术中心 Технический центр тяжелой техники. Тайюань			
Главный проектировщик									
Проверил		Проверка стандартов							
Директор института			Дата						