


HS00.90.5Z81X

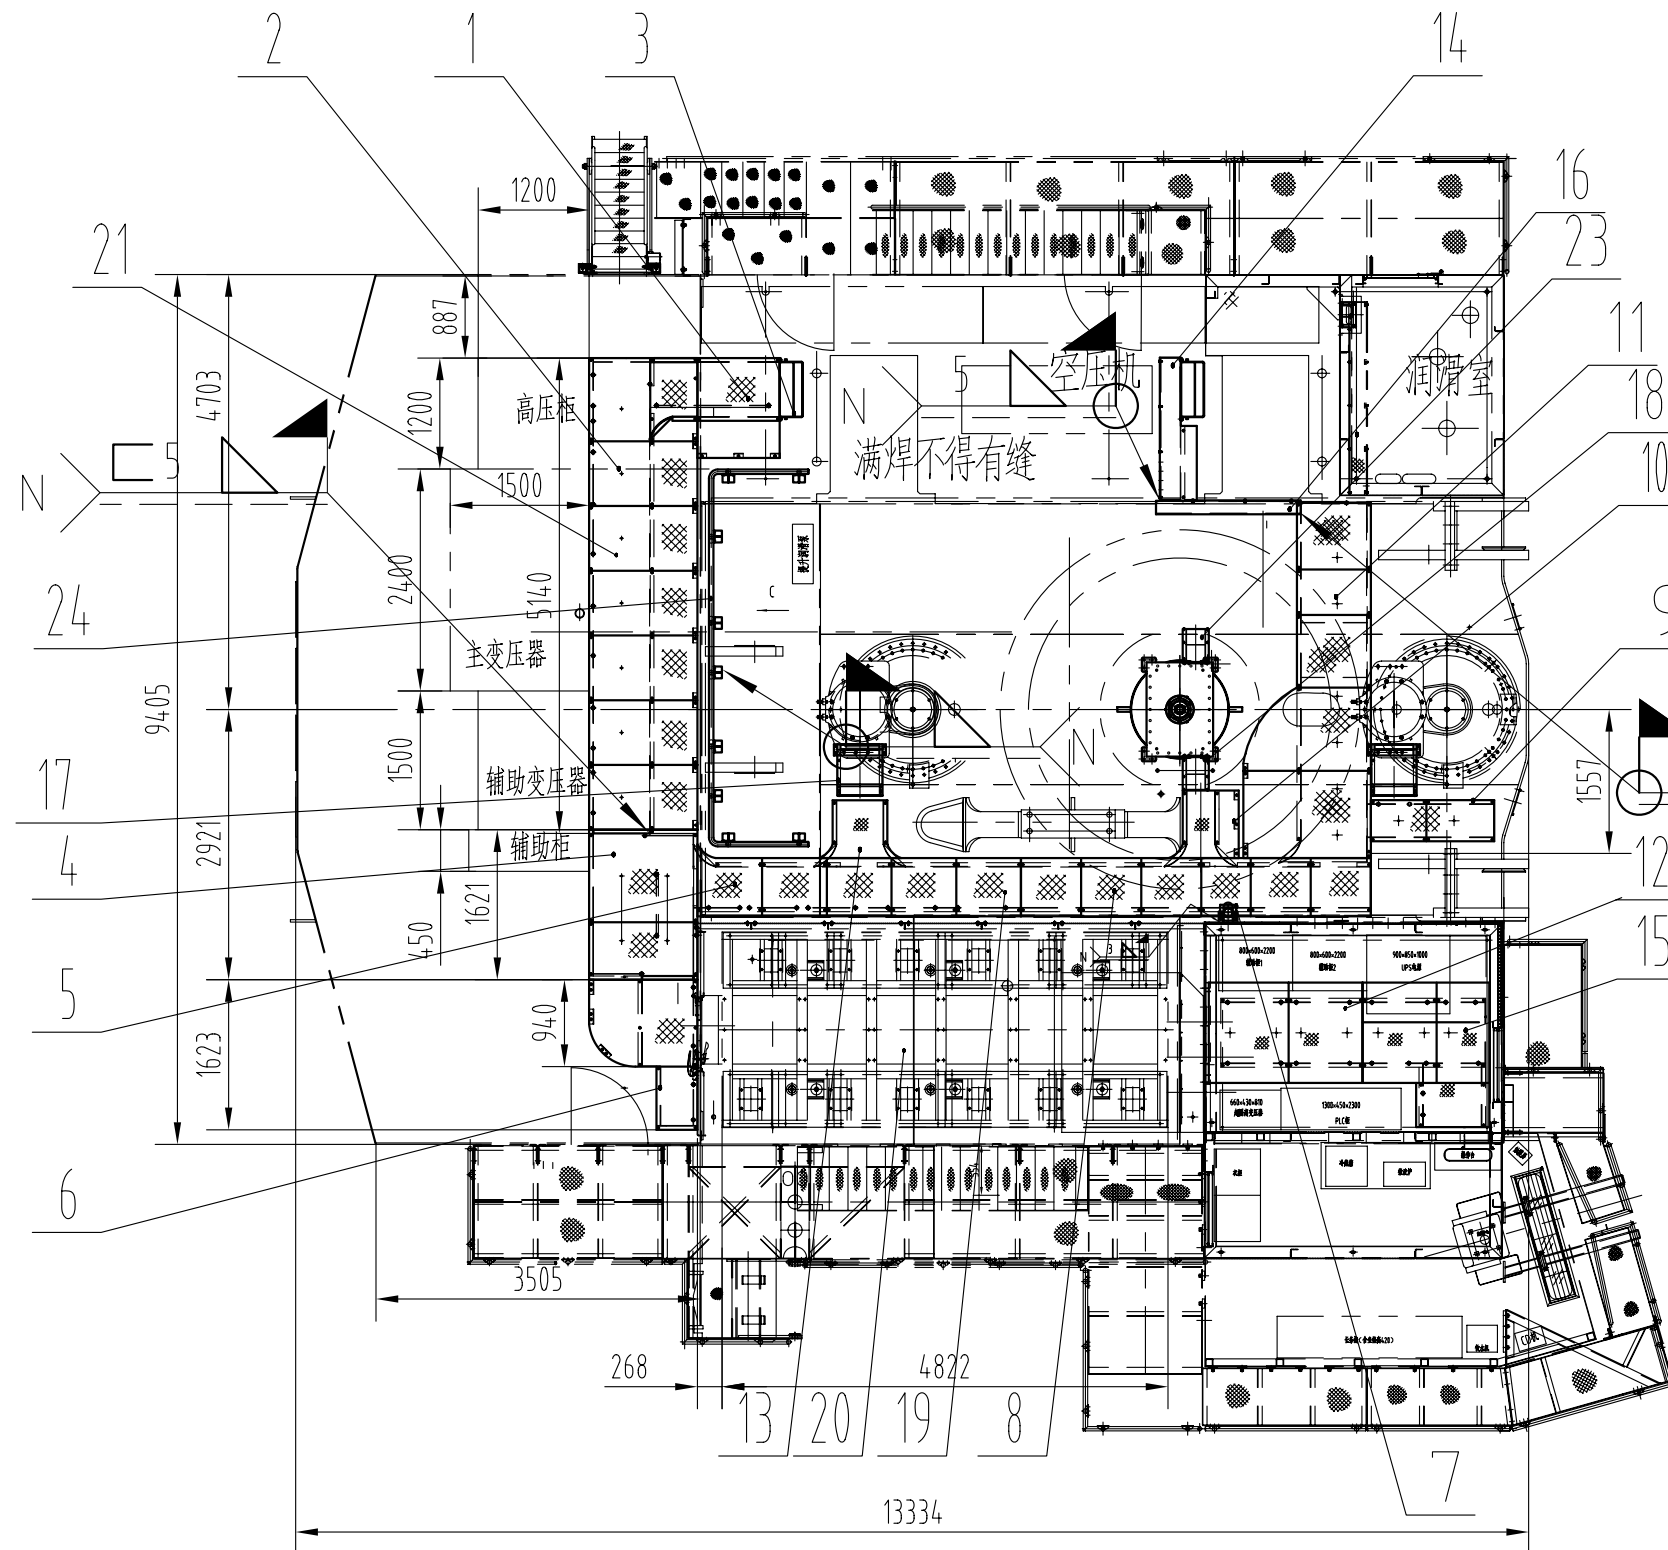

技术要求

1. 现场安装时将所有支撑焊管焊于平台上, 焊缝为
2. 地板安装后应平整, 地板之间的局部间隙不得大于5. 相互间的高度差不得大于5.
3. 地板与地板对接处, 在放置电缆之前, 现场安装时进行焊接, 焊高为5, 焊后打磨光滑, 不得有任何可能割线的棱边、毛刺, 与活盖板接触处不焊.
4. 若由于线槽错位无法焊接时, 在线槽对接处填设橡胶皮, 然后用胶水涂住.
5. 所有地板的走线槽上铺设橡胶板.
6. 序22用于保护电缆线, 在可能割线的地方放置橡胶板, 并将橡胶板固定后布线.
7. 本图规定了线槽的位置和部分电器柜的位置, 在电气布置时按此执行, 未规定部分见附件K1XXX.23.00中的相关图纸.


满焊不得有缝

Полной сварке нельзя иметь шов

Технические требования:

1. При монтаже на месте все фундаментные плиты привариваются к платформе, сварочные швы:
2. После монтажа фундаментных плит требуется выравнивание, локальные зазоры между полом не должны превышать 5. Отклонения высоты взаимного пространства не должны превышать 5.
3. При монтаже на площадке места стыковки фундаментных плит свариваются, высота сварки 5, после сварки проводится шлифовка, недопустимо наличие граней секущих линий, зазубрин, отсутствие сварки в местах контакта со съемным горизонтальным перекрытием.
4. Если невозможно провести сварку из-за неправильного расположения кабельного канала, то в месте его стыковки нужно проложить резину, а затем нанести клей.
5. Во все кабельные каналы, проходящие по полу, прокладываются резиновые пластины.
6. Деталь 22 используется для защиты электрокабеля, резиновые пластины устанавливаются в местах возможного обрыва кабеля, линии прокладываются после фиксации пластин.
7. На данном чертеже определено расположение кабельных каналов и части шкафов электроприборов. Прокладка электричества осуществляется в соответствии с этим расположением. Неуказанные части смотрите на соответствующем чертеже приложения K1XXX.23.00.

C向

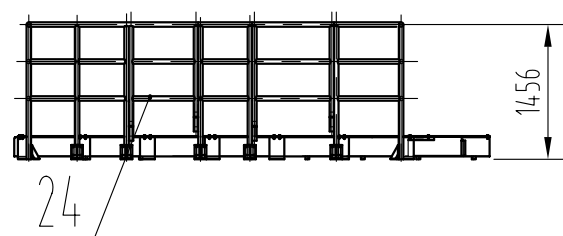

					活地板 Подвижный пол	K1825.06.00SH			
Отметка	Кол-во	Номер документа	Подпись	Дата					
Проектировщик		Технологическая проверка							
Контроль					通用技术条件 ОБЩЕПРИНЯТЫЕ ТЕХНИЧЕСКИЕ УСЛОВИЯ JB/T 5000	重量 Вес	3407.792	比例 Масштаб	1:1000
Главный проектировщик						共2张	Всего 2 листа	第1张	Лист1
Проверил		Проверка стандартов				 太重技术中心 Технический центр тяжелой техники, Тайюань			
Директор института		Дата							