


K1830.09.03.00SH

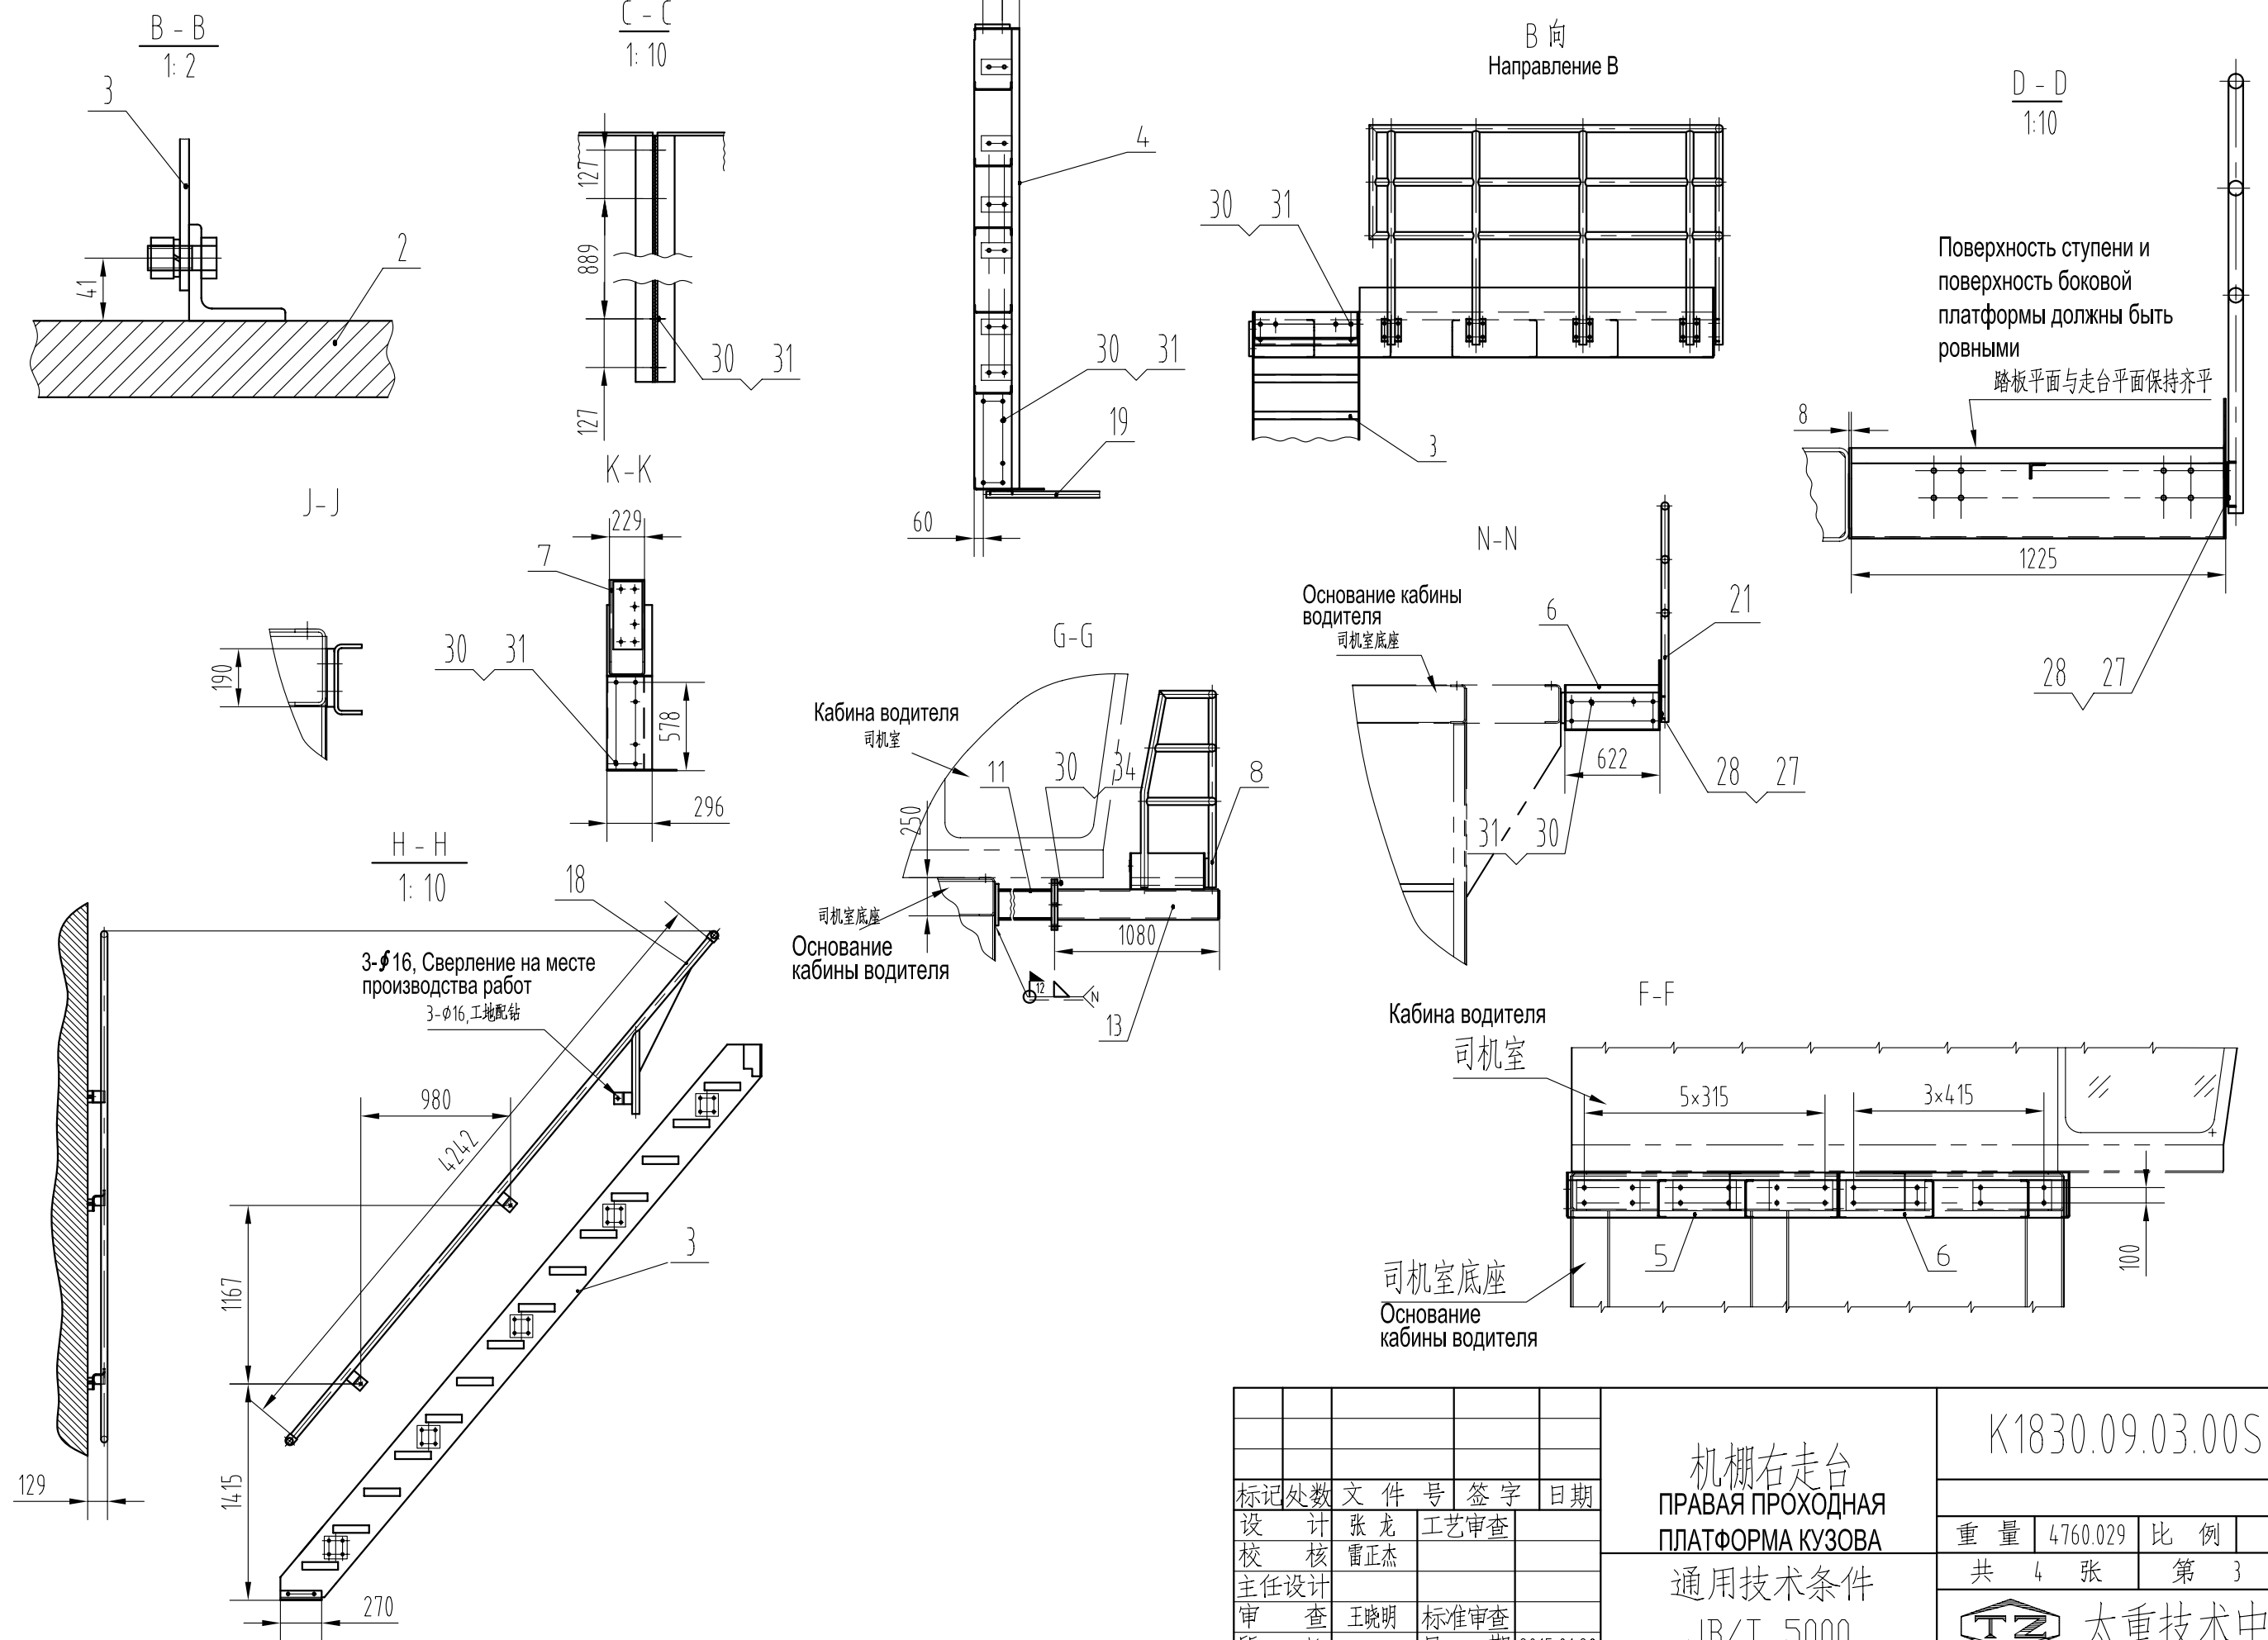

					机棚右走台 ПРАВАЯ ПРОХОДНАЯ ПЛАТФОРМА КУЗОВА 通用技术条件 JB/T 5000	K1830.09.03.00SH			
标记处数	文 件 号	签 字	日 期			重 量	4760.029	比 例	1:40
设 计	张 龙	工艺审查				共	4	张	第 3 张
校 核	雷正杰								
主任设计									
审 查	王晓明	标准审查							
所 长		日 期	2015.01.20		 太重技术中心				