
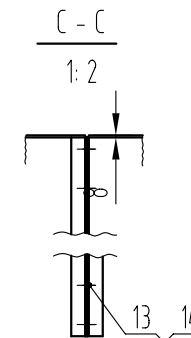
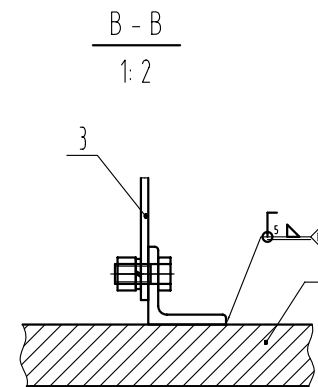
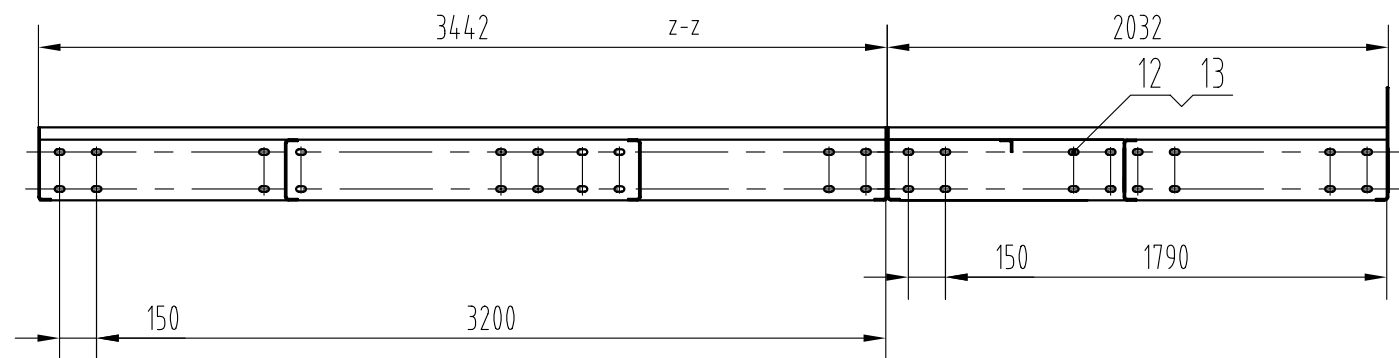


K1830.09.07.00SH

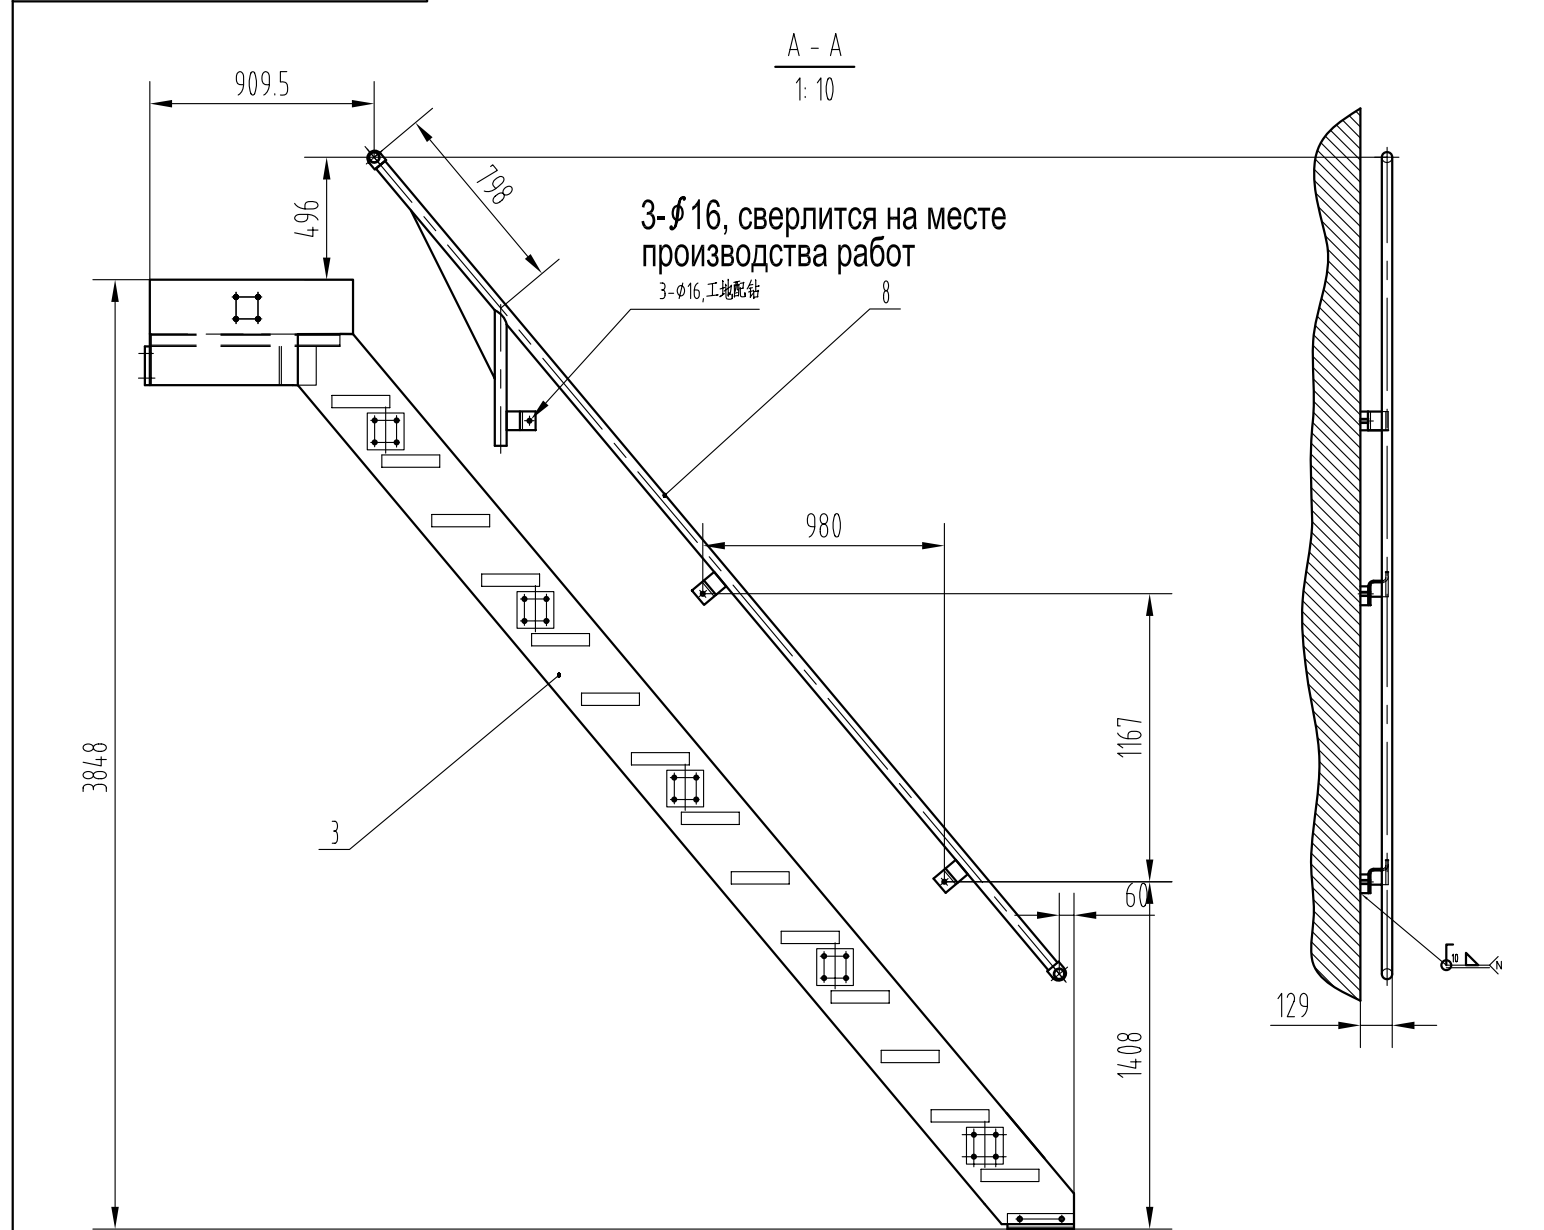

Коннектор	15	K1812.09.07.09.00	连接器	1	
Болт M20x45	14	GB/T5783	螺栓M20X45	6	
Контровочная гайка M20	13	GB/T889.1	螺母M20	42	
Болт M20x65	12	GB/T5783	螺栓M20X65	36	
Контровочная гайка M12	11	GB/T889.1	螺母M12	64	
Болт M12x40	10	GB/T5783	螺栓M12X40	64	
Опора	9	K1801.09.07.09.00	支架	1	
Перила	8	K1830.09.07.08.00	栏杆	1	
Перила	7	K1830.09.07.07.00	栏杆	1	
Перила	6	K1830.09.07.06.00	栏杆	1	
Перила	5	K1830.09.07.05.00	栏杆	1	
Перила	4	K1830.09.07.04.00	栏杆	1	
Лестница	3	K1830.09.07.03.00	梯子	1	
Проходная платформа	2	K1830.09.07.02.00	走台	1	
Лестница	1	K1830.09.07.01.00	梯子	1	

					№	Обозначение	Наименование				Кол-во	Примечания
							K1830.09.07.00SH					
标记	处数	文 件 号	签 字	日期	LEВАЯ ПРОХОДНАЯ ПЛАТФОРМА КУЗОВА	机棚左走台 通用技术条件 JB/T 5000	重 量	1774.452	比 例	1:30	 太重技术中心	
设 计	张 龙	工艺审查					共	2 张	第	2 张		
校 核	雷正杰											
主任设计												
审 查	王 晓 明	标准审查										
所 长		日 期	2015.01.20									