


K1812.11.35.00SH

技术要求

1. 厂内预装时即将安装底板焊在机棚顶部。
2. 现场在夹缝中涂足够的密封胶后，将防雨槽把合在安装地板上。

Технические требования

1. Во время предварительной сборки на заводе нижняя монтажная панель приваривается к верхней части кузова.
2. На площадке во все щели заливается нужное количество герметика, желоб защиты от дождя соединяется с нижней монтажной панелью.

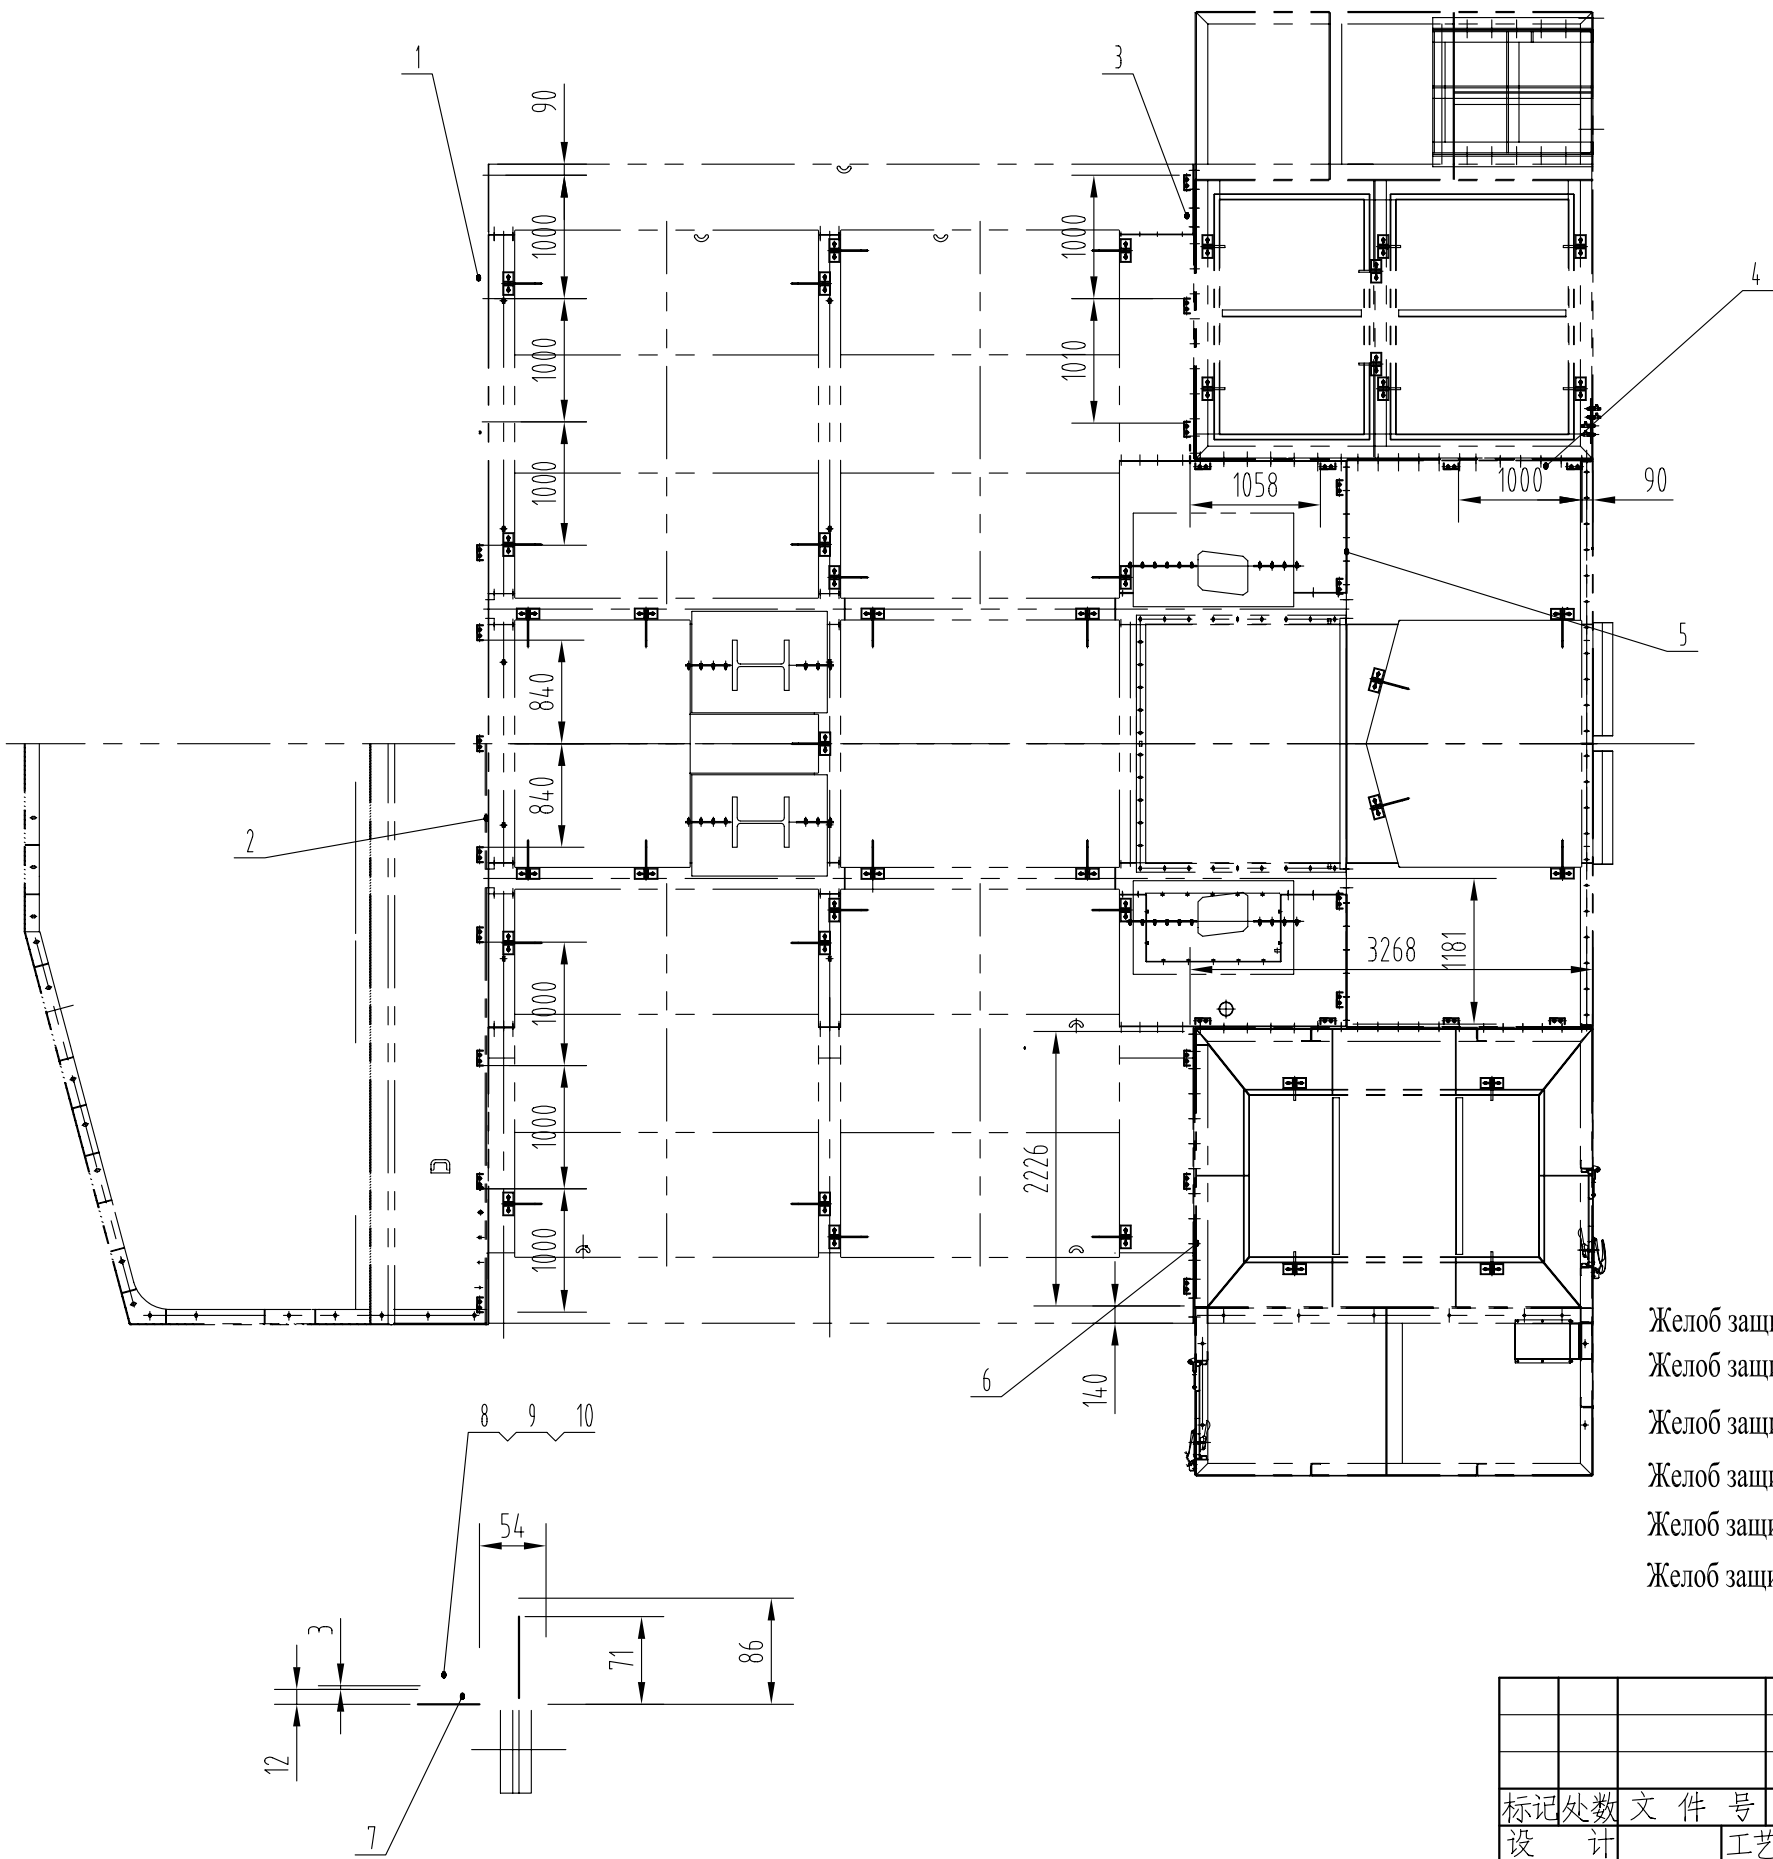

Шайба 10
Шайба 10
Болт М10х20

Желоб защиты от дождя 6
Желоб защиты от дождя 5
Желоб защиты от дождя 4
Желоб защиты от дождя 3
Желоб защиты от дождя 2
Желоб защиты от дождя 1

10	GB/T93	垫圈10	58	
9	GB/T97.1	垫圈10	116	
8	GB/T5783	螺栓M10X20	58	
7	K1812.11.35.07	-12X50X120	29	
6	K1812.11.35.06	防雨槽6	1	
5	K1812.11.35.05	防雨槽5	2	
4	K1812.11.35.04	防雨槽4	2	
3	K1812.11.35.03	防雨槽3	1	
2	K1812.11.35.02	防雨槽2	1	
1	K1812.11.35.01	防雨槽1	2	
序号	代 号	名 称	数量	备 注

						№ Обозначение 机棚顶部防雨槽 Желоб защиты от жогдя верхней части кузова 通用技术条件 JB/T 5000	Наименование		Кол-во		Примечания	
							K1812.11.35.00SH					
标记处数	文 件 号	签 字	日期				重 量	142.12	比 例	1:60		
设 计		工艺审查					共	张	第	张		
校 核												
主任设计												
审 查		标准审查										
所 长		日 期				 太重技术中心						