


K1838.90.02.00SH

标记	处数	文件号	签字	日期

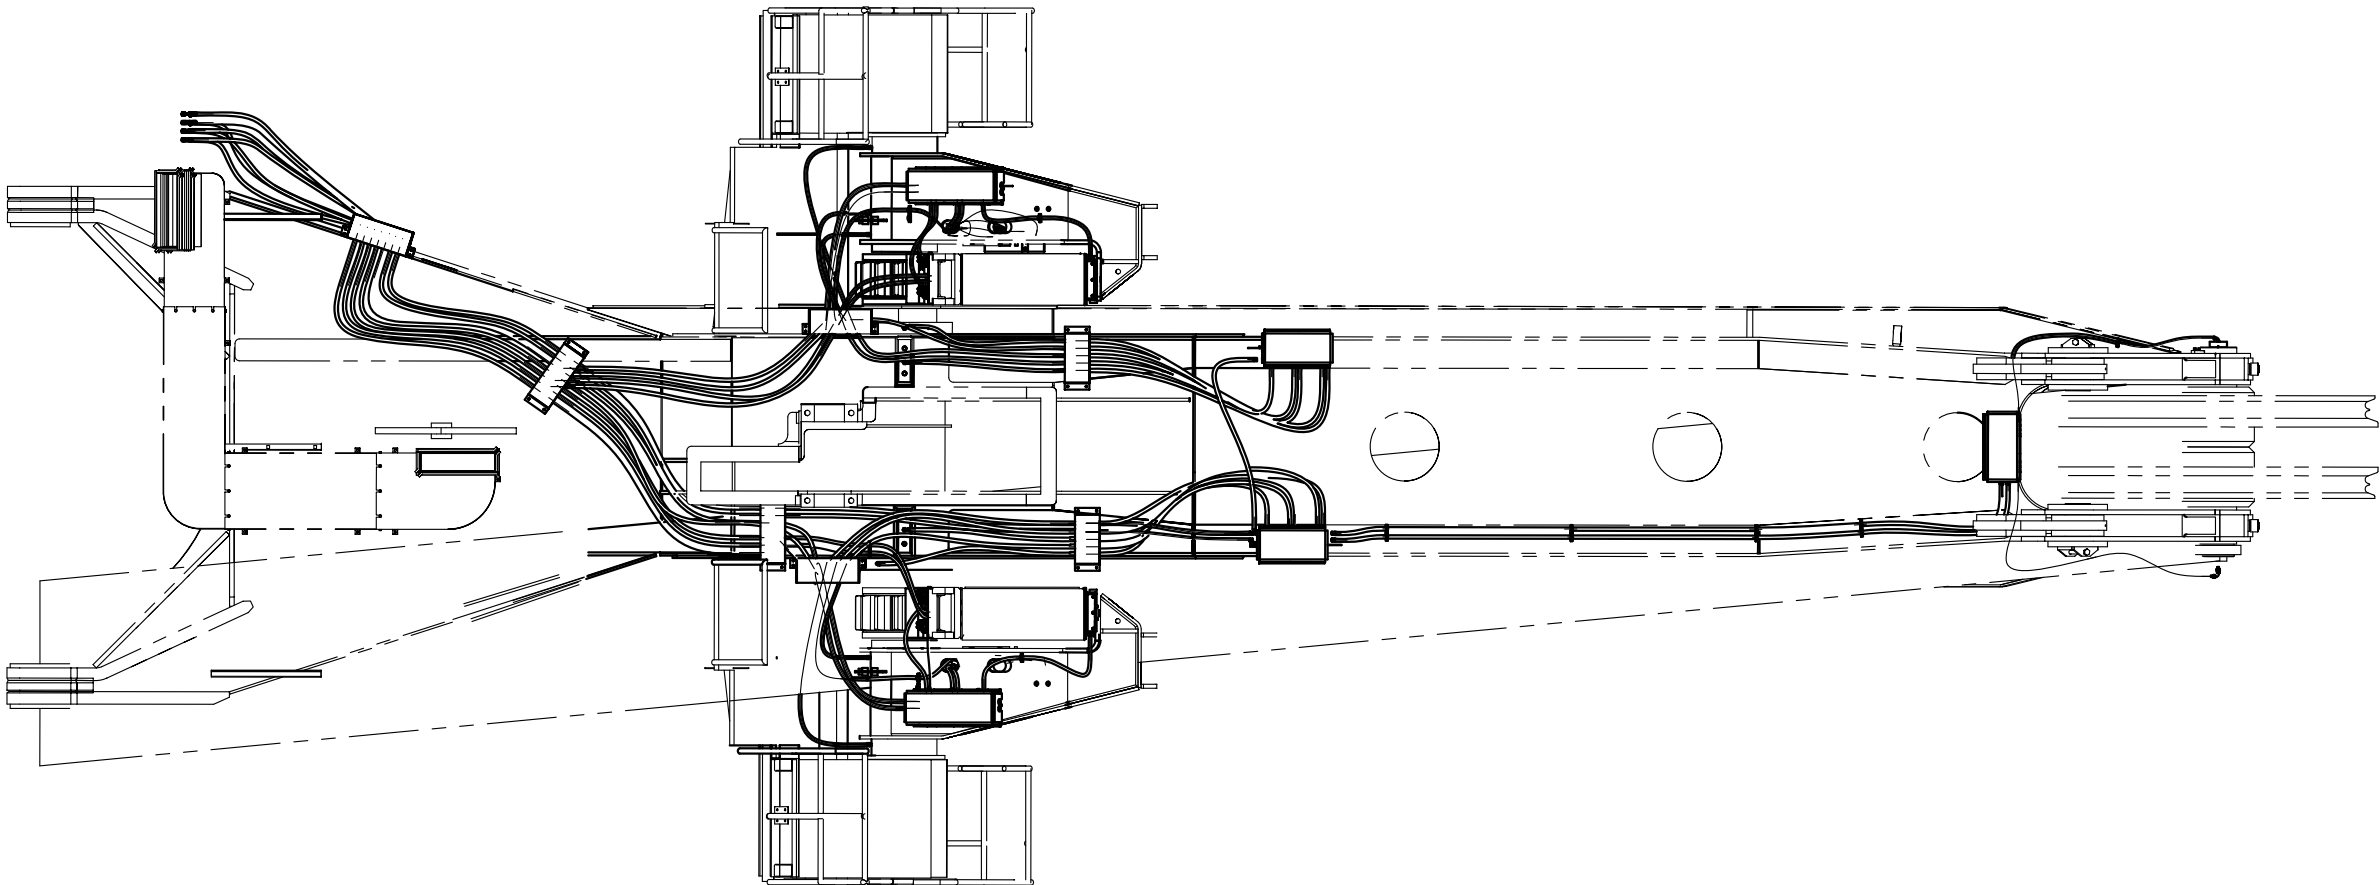

24	K1622.90.02.03.00	斗杆上平面喷射		2
23	3735050000	快速排气阀	Скоростной воздухоспускной клапан	1
22	8MJ-10FJX	直通接头	Торцевой цилиндрический соединитель	20
21	10MJ-10MJ-10FJX	三通管接头	Трехходовое соединение	2
20	8MJ-8MJ-8FJX	三通接头	Трехходовое соединение	6
19	JB/ZQ4492	单管夹 28	Трубный зажим 28	18
18	8MJ-6MT	端直通接头	Торцевой цилиндрический соединитель	12
17	K1838.90.02.02	大臂气路胶管总成	Резиновые шланги смазки в сборе	1
16	K1838.90.02.01	大臂润滑胶管总成	Пневматические резиновые шланги в сборе	1
15	k1838.90.02.15.00	保温罩三	защитный кожух для теплозащиты	2
14	k1838.90.02.14.00	保温罩二	защитный кожух для теплозащиты	2
13	k1838.90.02.13.00	保温罩一	защитный кожух для теплозащиты	3
12	K1838.90.02.12.00	管路连接板六	Соединительная панель 6 трубопроводов	1
11	K1838.90.02.11.00	大臂伴热保温施工	частный вид сопроводительного подогрева и теплозащиты	1
10	K1838.90.02.10.00	管路连接板五	Соединительная панель 5 трубопроводов	1
9	K1838.90.02.09.00	管路连接板四	Соединительная панель 4 трубопроводов	2
8	K1838.90.02.08.00	管路连接板三	Соединительная панель 3 трубопроводов	2
7	K1838.90.02.07.00	管路连接板二	Соединительная панель 2 трубопроводов	2
6	K1838.90.02.06.00	管路连接板一	Соединительная панель трубопроводов 1	1
5	K1838.90.02.05.00	分配器组件二	Сборка 2 распределителя	3
4	K1838.90.02.04.00	分配器组件一	Сборка 1 распределителя	2
3	K1838.90.02.03.00	右侧斗杆喷射组件		1
2	K1838.90.02.02.00	左侧斗杆喷射组件		1
1	K1838.90.02.01.00	推压喷射组件		2

P001001247-A				大臂集中润滑布置 Устройство центральной смазки стрелы	K1838.90.02.00SH			
设 计	郭世英	工艺审查	袁运星					
校 核	卢安卿			通用技术条件 JB/T 5000				
审 查	张玉姝	标准审查	白焱		重 量 98.62 比 例 1:60			
主任设计		主管主任			共 3 张 第 2 张			
所 长					 太重技术中心			
日 期	20161209							