


K1838.92.02.00SH

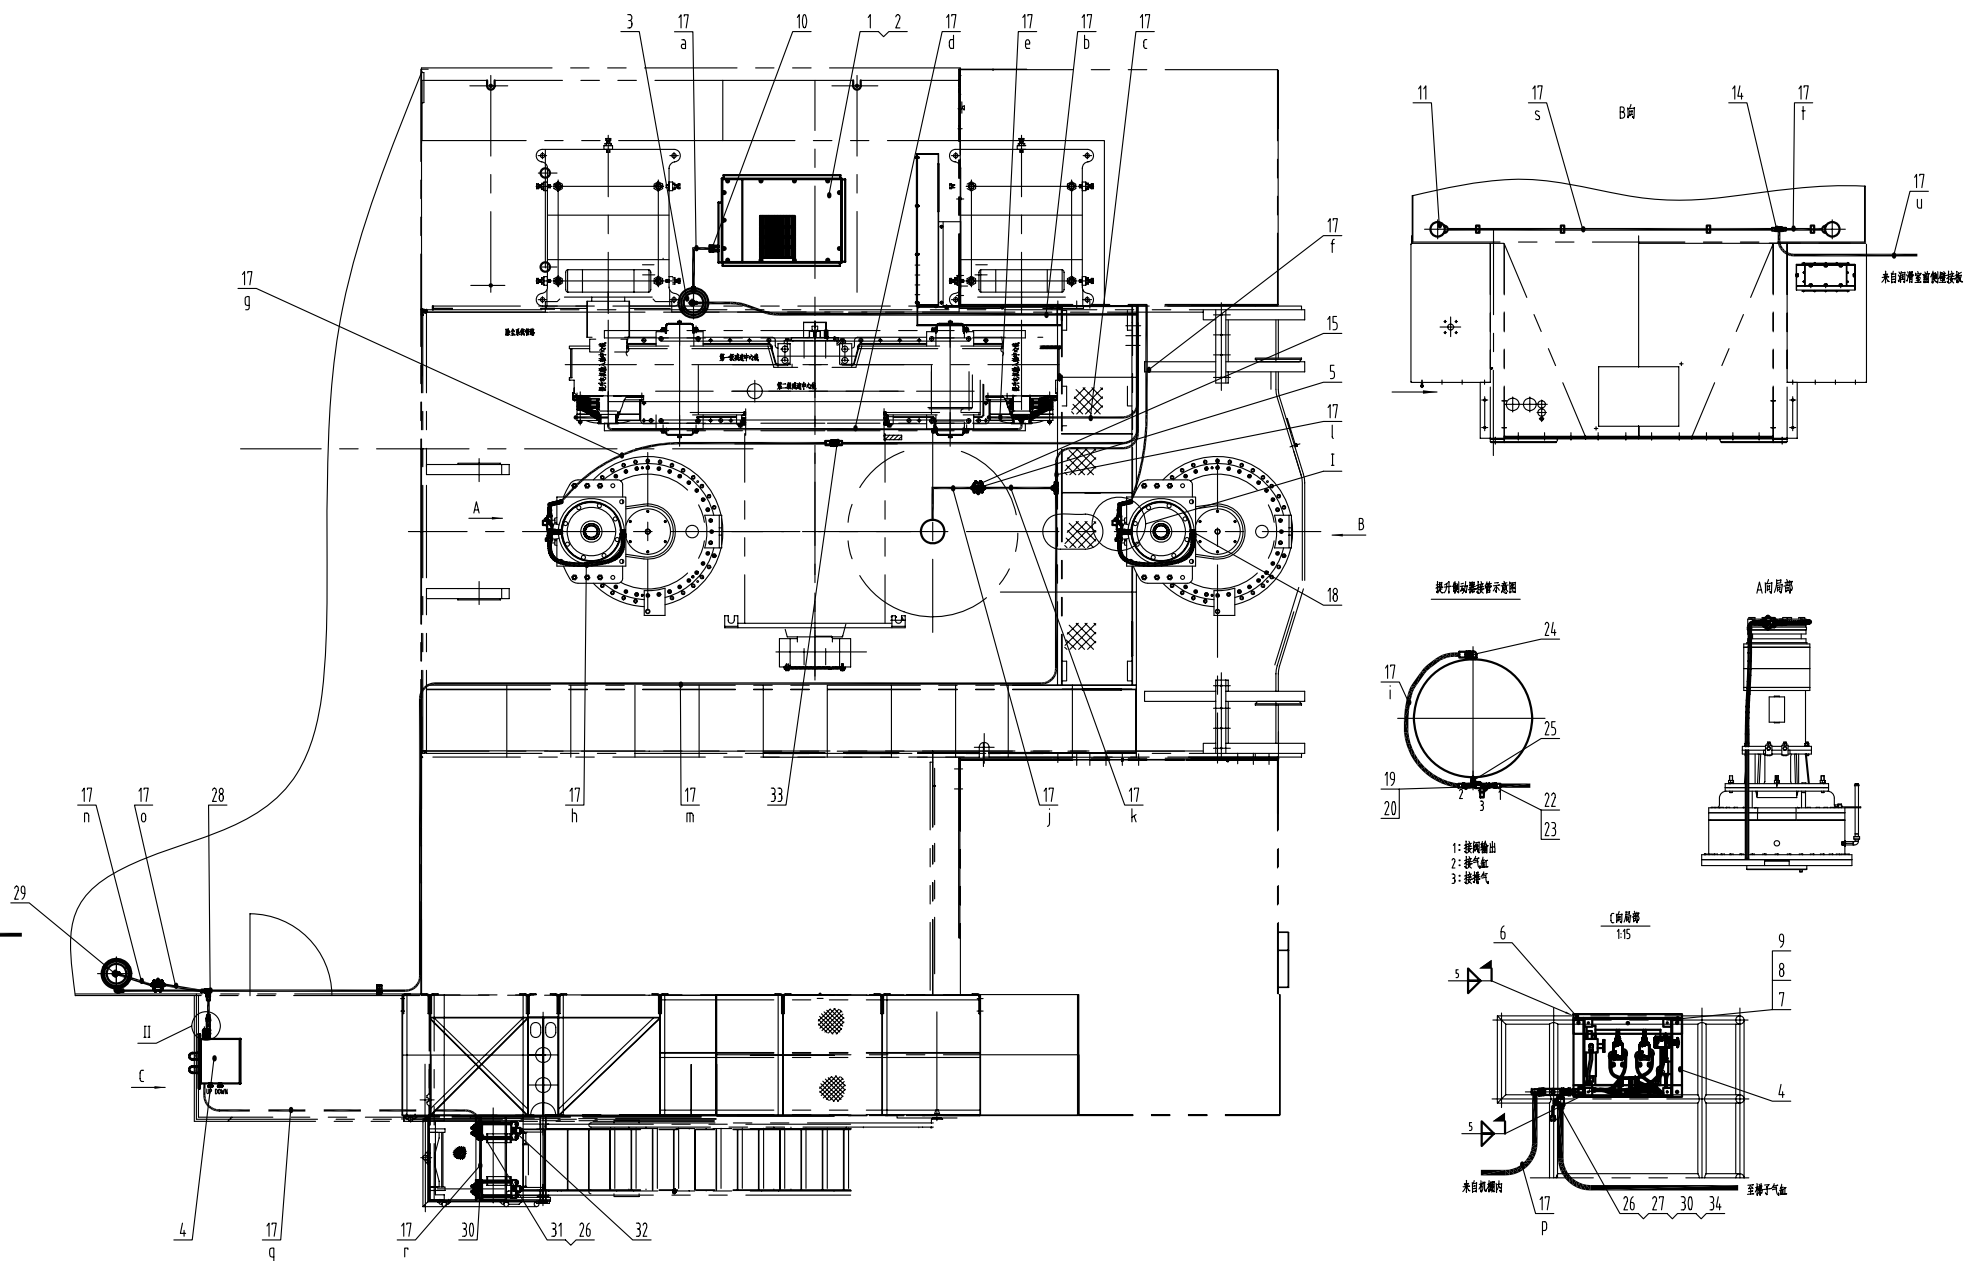

技术要求

1. 本图所示为平台压气系统所属部分的布置方案,各管夹安装轨按图示尺寸制作并在安装时焊接于图示位置。
2. 图示气路管路规格详见表格图。各管路长度供参考,采用扣压设备扣压成胶管总成后安装。
3. 在相应元件处采用标签标示控制元件代码(见K1838.92.00第二张电液委托),要求美观大方耐污。

34	SD1/2	球阀	1	
33	10MJ-10MJ	直通过接头	10	
32	FXS-R1/2	消声器	2	
31	10MJ-10FJX-10MJ	三通管接头	1	
30	10MJ-8MT9	直角接头	2	
序号	代 号	名 称	数量	备注

P001003850-A			
设 计	卢安卿	工艺审查	袁运星
校 核	吕晓林		
审 查	张玉姝	标准审查	白焱
主任设计		主管主任	
所 长			
日 期	20161209		

标记	处数	文件号	签字	日期

29	10MJ-12MT	端直通过接头	2	
28	10MJ-10BKHD-LN	隔板接头	1	
27	10FJX-10FJX	直通过接头	2	
26	10MJ-8MT	端直通过接头	8	
25	12MP-16FJX	端直通过接头	2	
24	12MJ-12MT9	直角接头	2	
23	10MJ-12FJX	端直通过接头	4	
22	12MJ-16MP	端直通过接头	4	
21	8MT-12FJX	端直通过接头	2	
20	12MJ-16FJX	端直通过接头	4	
19	16MJ-16MJ-16MP	三通接头	4	
18	12MJ-8MT9	直角接头	2	
17	K1838.92.02.01	气动胶管总成	1	
16	FXS-NPT1	消声器	4	
15	10MJ-22MML	端直通过接头	4	
14	10MJ-10MJ-10MJ	三通接头	4	
13	3735050000	快速排气阀	4	
12	3451300000	节流阀	1	
11	TZQ7348.1	双音气喇叭	2	
10	12MJ-16MT	端直通过接头	1	
9	GB/T93	垫圈 10	4	
8	GB/T6170	螺母 M10	4	
7	GB/T5783	螺栓 M10X30	4	
6	K1622.92.02.03	安装板	2	
5	K1623.92.02.06.00	防冻器装置	2	
4	K1623.92.02.05.00	气动梯子控制箱	1	
3	K1838.92.02.02.00	气水分离器组件	2	
2	K1622.92.02.02.00	空压机安装底座	1	
1	K1838.92.02.01.00	空压机装置	1	

序号	代 号	名 称		数量	备 注
平台气路布置		K1838.92.02.00SH			
КОМПОНОВКА ПНЕВМОПРОВОДОВ ПЛАТФОРМЫ					
		重 量	342.58	比 例	1:75
通用技术条件 JB/T 5000		共 2 张		第 1 张	
		 太重技术中心			