


标记	处数	文件号	签字	日期

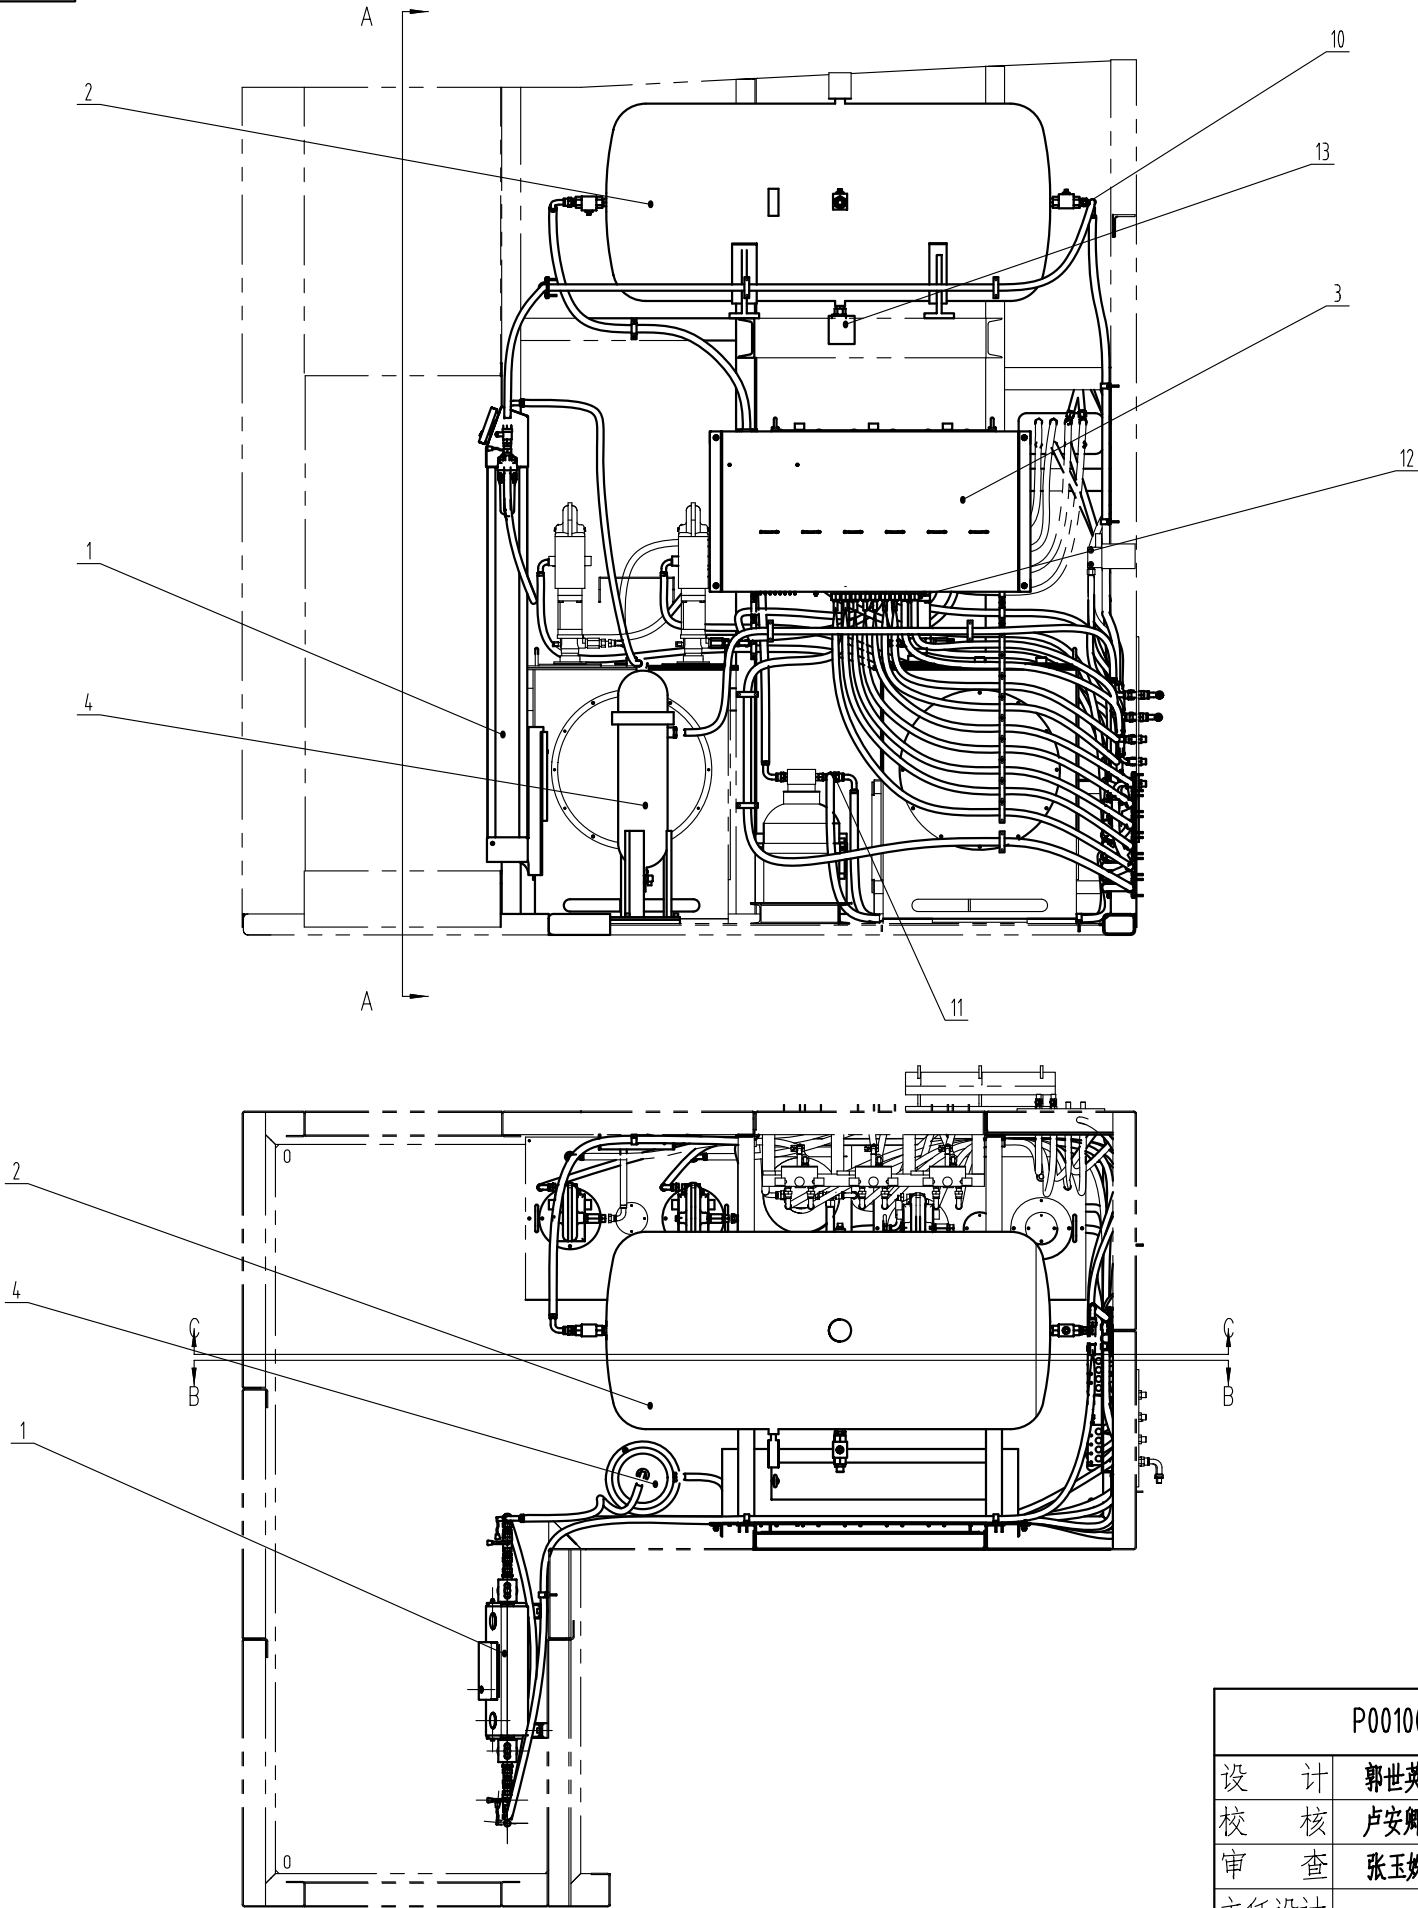

技术要求

润滑室内胶管不作保温处理。图示管线显示各连接管道走向和方位，胶管长度允许稍作调整。

管线接口参照气动原理图要求。管路要求用管夹固定，不得过度张紧，要留下热胀冷缩的余量。

管线安装前用压缩空气吹净灰尘等杂物。未安装前管路放置在温暖的库房内，不得露天堆放。

13	MIC-A-Rc1/2-AC220V50Hz	电子排水阀	1	
12	10MJ-8MT	端直通管接头	11	
11	10MJ-10MJ-10FJX	三通管接头	2	
10	10MJ-10FJX-10MJ	三通管接头	2	
9	K1623.92.01.05.00	补脂减压阀装置	1	
8	PA1000/B0016PQ242G14MM	压力传感器	1	
7	23350 100 G1/2 量程 0~16bar +821.21	双电接点压力表	1	
6	JB/ZQ4492	单管夹 28	20	
5	K1838.92.01.01	润滑室内气路胶管总成	1	
4	K1838.92.02.02.00	气水分离器组件	1	
3	K1623.92.01.01.00	上部气路控制箱	1	
2	K1892.92.01.02.00	主气路气包	1	
1	K1838.92.01.01.00	干燥机装置	1	
序号	代 号	名 称	数量	备 注

P001000949-A				润滑室内气路布置 Компоновка		K1838.92.01.00SH			
设 计	郭世英	工艺审查	袁运星						
校 核	卢安卿			пневмосистемы внутри помещения					
审 查	张玉姝	标准审查	白焱			重 量 138.25 比 例 1:30			
主任设计		主管主任		通用技术条件 JB/T 5000		共 3 张		第 1 张	
所 长						 太重技术中心			
日 期	20161209								