
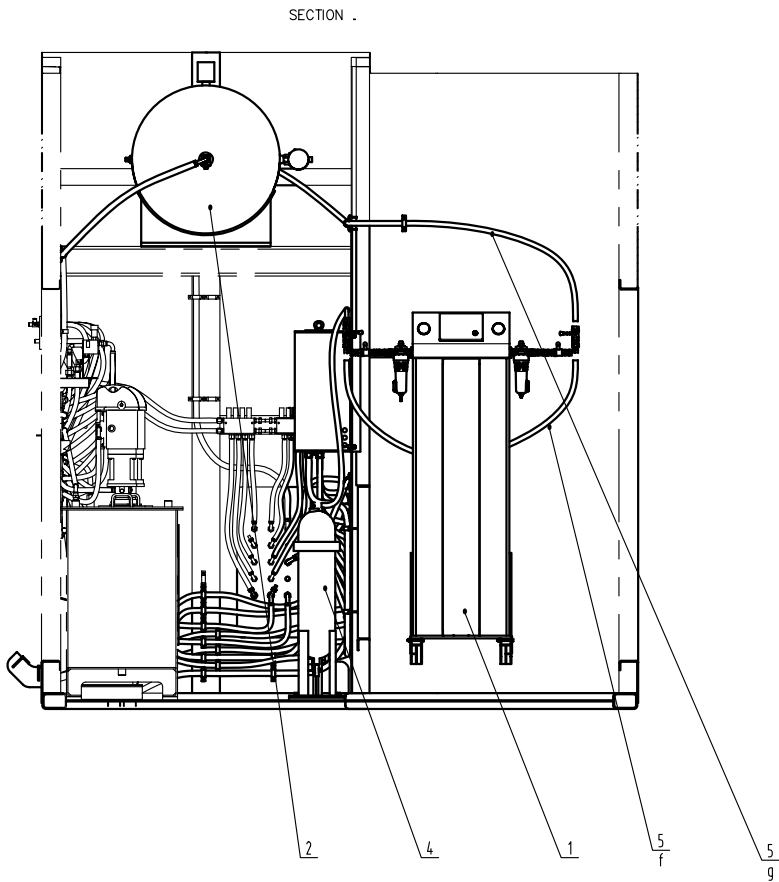


标记	处数	文件号	签字	日期

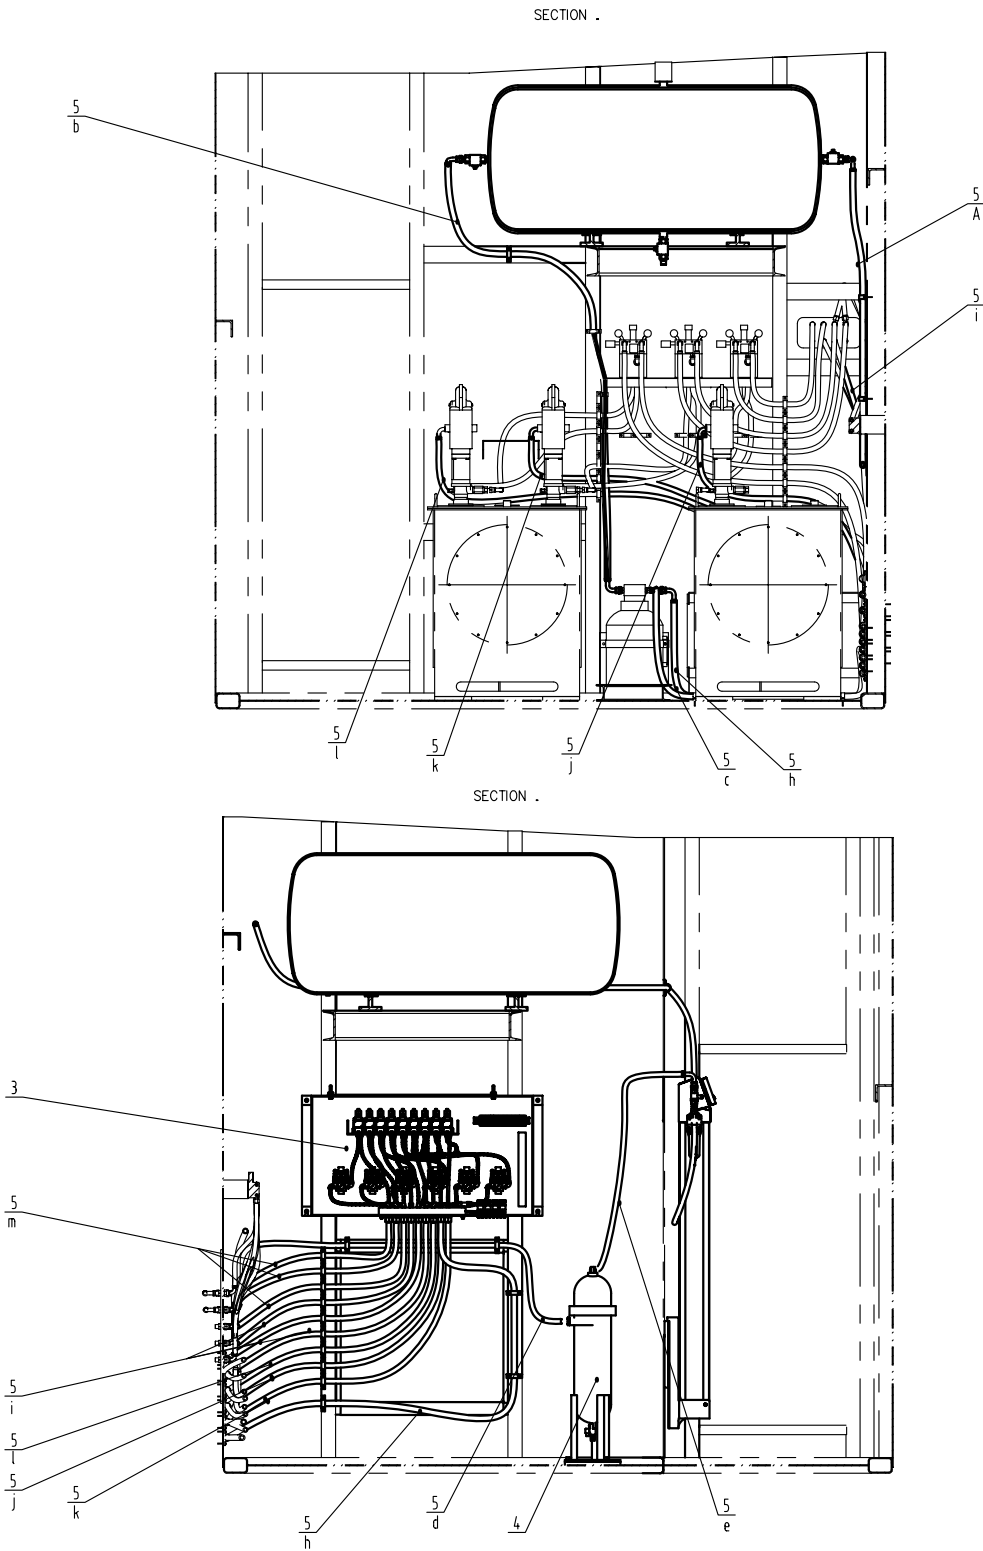

- Технические требования
- Данный чертеж - это план компоновки узлов системы сжатого воздуха в смазочной камере. Монтажные балки трубных зажимов изготавливаются в соответствии с размерами, указанными на чертеже, и во время монтажа привариваются в местах, показанных на чертеже.
 - Подробные параметры трубопроводов смазки см. на чертеже с таблицей. Длина всех трубопроводов дана для справки. Оборудование задержки давления монтируется после сборки всех шлангов задержки давления.
 - Указанные на чертеже модели шлангов - это модели Северо-западного резинового завода, /неразборчиво из-за ошибки в изображении/.
 - Внутренний диаметр шлангов - 16/19, внешний - 24/28, рабочее давление 13/10 МПа. Соединение шлангов - по американской системе JIC с внутренней конической поверхностью 740 и внутренней резьбой, отвечает стандарту SAEJ514 Трубные зажимы направляющего типа. Соответствуют стандарту DIN3015.

P001000949-A				润滑室内气路布置		K1838.92.01.00SH				
设 计	郭世英	工艺审查	袁运星	Компоновка пневмосистемы внутри помещения						
校 核	卢安卿									
审 查	张玉姝	标准审查	白焱							
主任设计		主管主任		通用技术条件 JB/T 5000		重 量		138.25	比 例	1:40
所 长						共 3 张		第 2 张		
日 期	20161209							 太重技术中心		