


HS00'E6'8E8LX

标记	处数	文件号	签字	日期

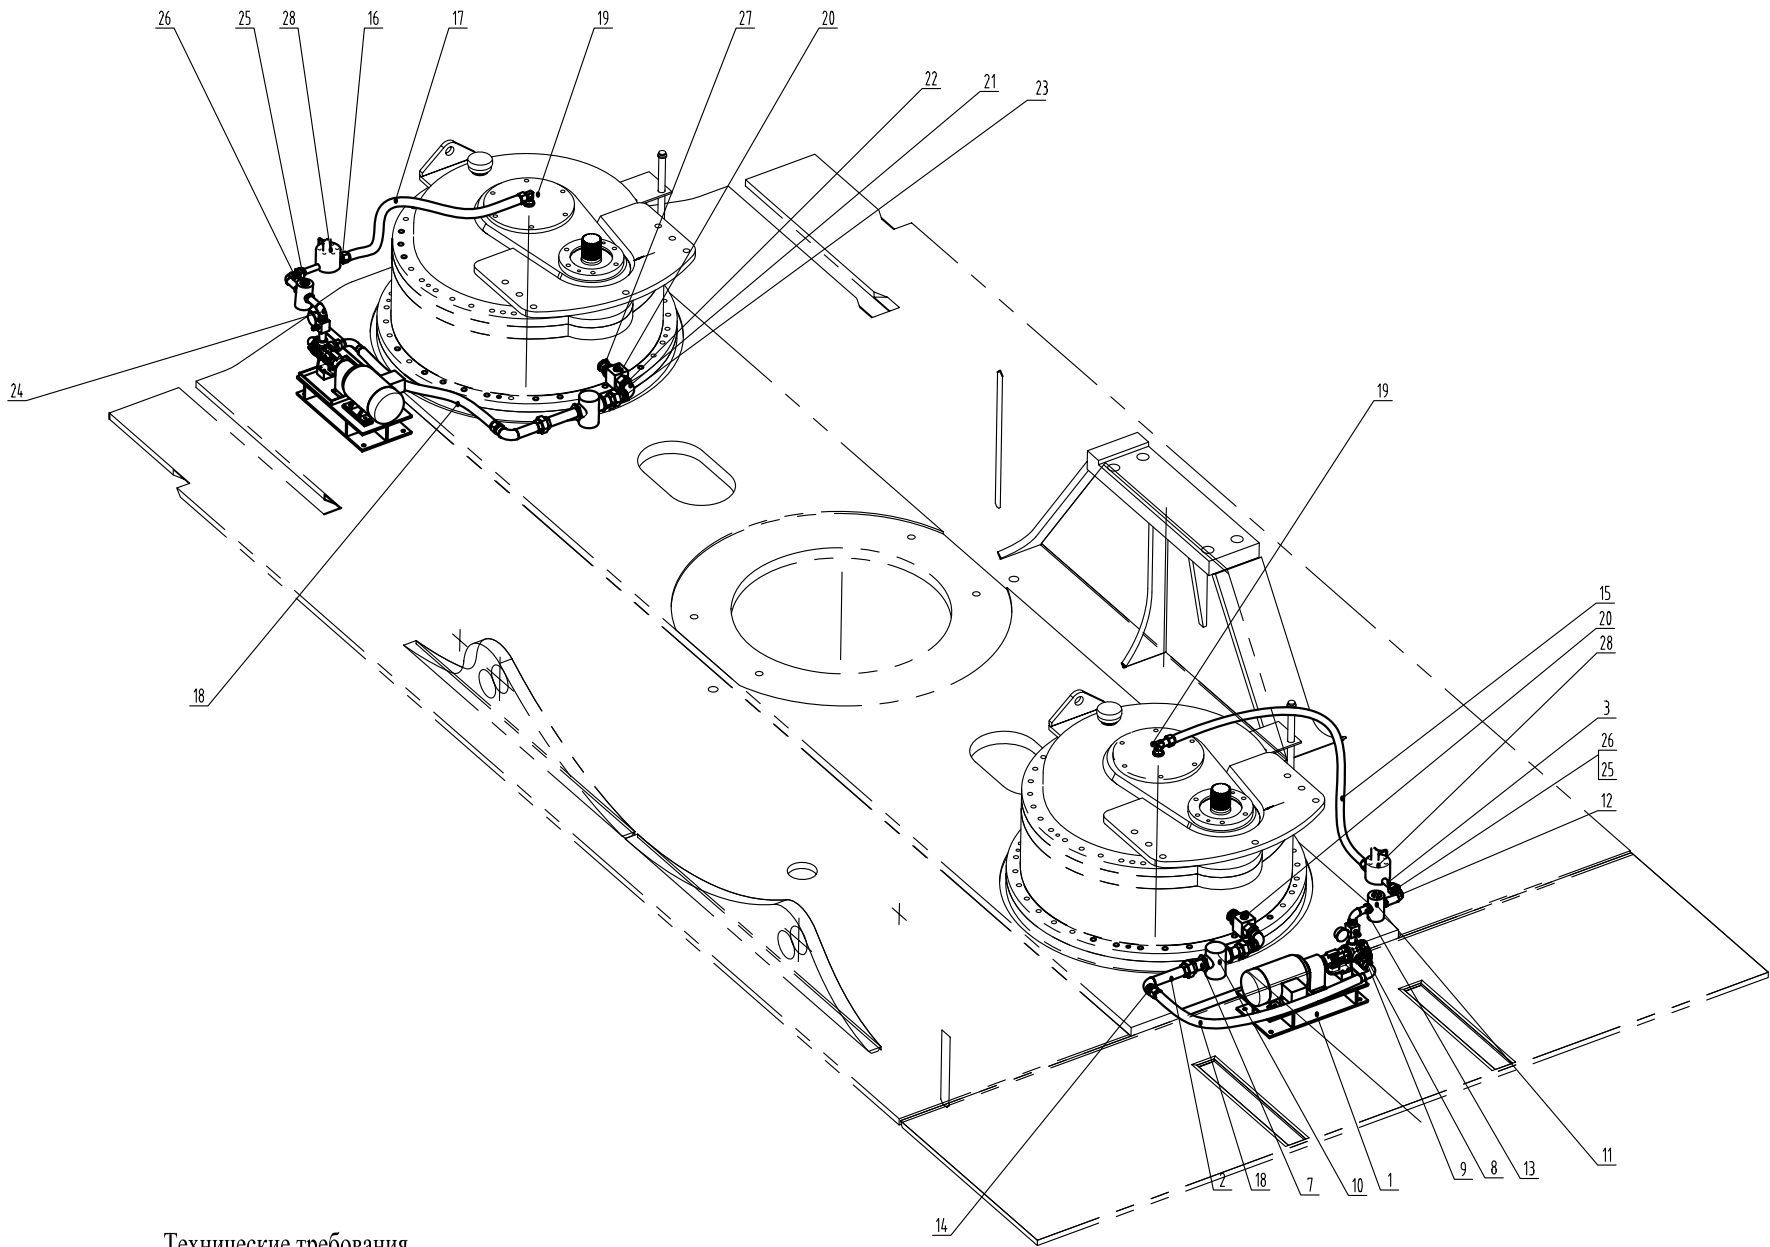

Технические требования

На данном чертеже изображены направления трубопроводов с точками впрыскивания смазки редуктора поворота WK-35. Во время сборки на площадке они фиксируются на внешнем корпусе редуктора точечной сваркой. Шланги на корпусе коробки фиксируются с помощью трубных зажимов. Длина между соединениями каждой трубы определяется в соответствии с требованиями на площадке.

28	DWE-FGR200G34A3TS75L	齿轮流量计	2	
27	GB/T3287	内外螺丝 N4-2X(1+1/2)-Zn-B	2	
26	GB/T3287	内接头 N8-3/4-Zn-C	2	
25	GB/T3287	活接头 U1-3/4-Zn-D	2	
24	GB/T3287	弯头 A1-1-Zn-C	2	
23	N8(280)-1.1/2-Zn-A	内接头	6	
22	GB/T3287	活接头 U1-1.1/2-Zn-C	4	
21	GB/T3287	弯头 A1-1.1/2-Zn-C	4	
20	Q11F-16P-1.1/2"	低压球阀	2	
19	16MJ-20MT9	管接头	2	
18	1SN32-1250/20-20FJX/20-20FJX9	胶管总成	2	
17	1SN25-1600/16-16FJX/16-16FJX	胶管总成	1	
16	16MJ-16MT9	管接头	2	
15	1SN25-2500/16-16FJX/16-16FJX	胶管总成	1	
14	20MJ-24MT	端直通接头	2	
13	20MJ-16MP	端直通管接头	2	
12	GB/T3287	内接头 N8(280)-1-Zn-A	2	
11	F-1010-IIRN-016	过滤器	2	
10	F-1015-IIRN-013带磁棒	出油过滤器	2	
9	K1892.91.02.00	测压装置	2	
8	K1892.93.02	连接管R1-NPT1	2	
7	K1892.93.01	连接管R1.1/2-NPT1.1/2	4	
6	K1838.93.05	40管支架	2	
5	K1838.93.04	20管支架	2	
4	K1838.93.03	25管支架	2	
3	K1838.93.02	接管20	2	
2	K1838.93.01	接管40	2	
1	K1838.93.01.00	回转油泵电机装置	2	
序号	代 号	名 称	数量	备 注

P001000964-A				回转减速机润滑		K1838.93.00SH			
设 计	郭世英	工 艺 审 查	袁运星	СИСТЕМА СМАЗКИ РЕДУКТОРА ПОВОРОТА					
校 核	卢安卿								
审 查	吕晓林	标准审查	白焱			重 量	217.36	比 例	1:25
主任设计		主管主任		通用技术条件 JB/T 5000		共 3 张		第 1 张	
所 长			 太重技术中心						
日 期	20161209								