


K1838.93.00SH

标记	处数	文件号	签字	日期

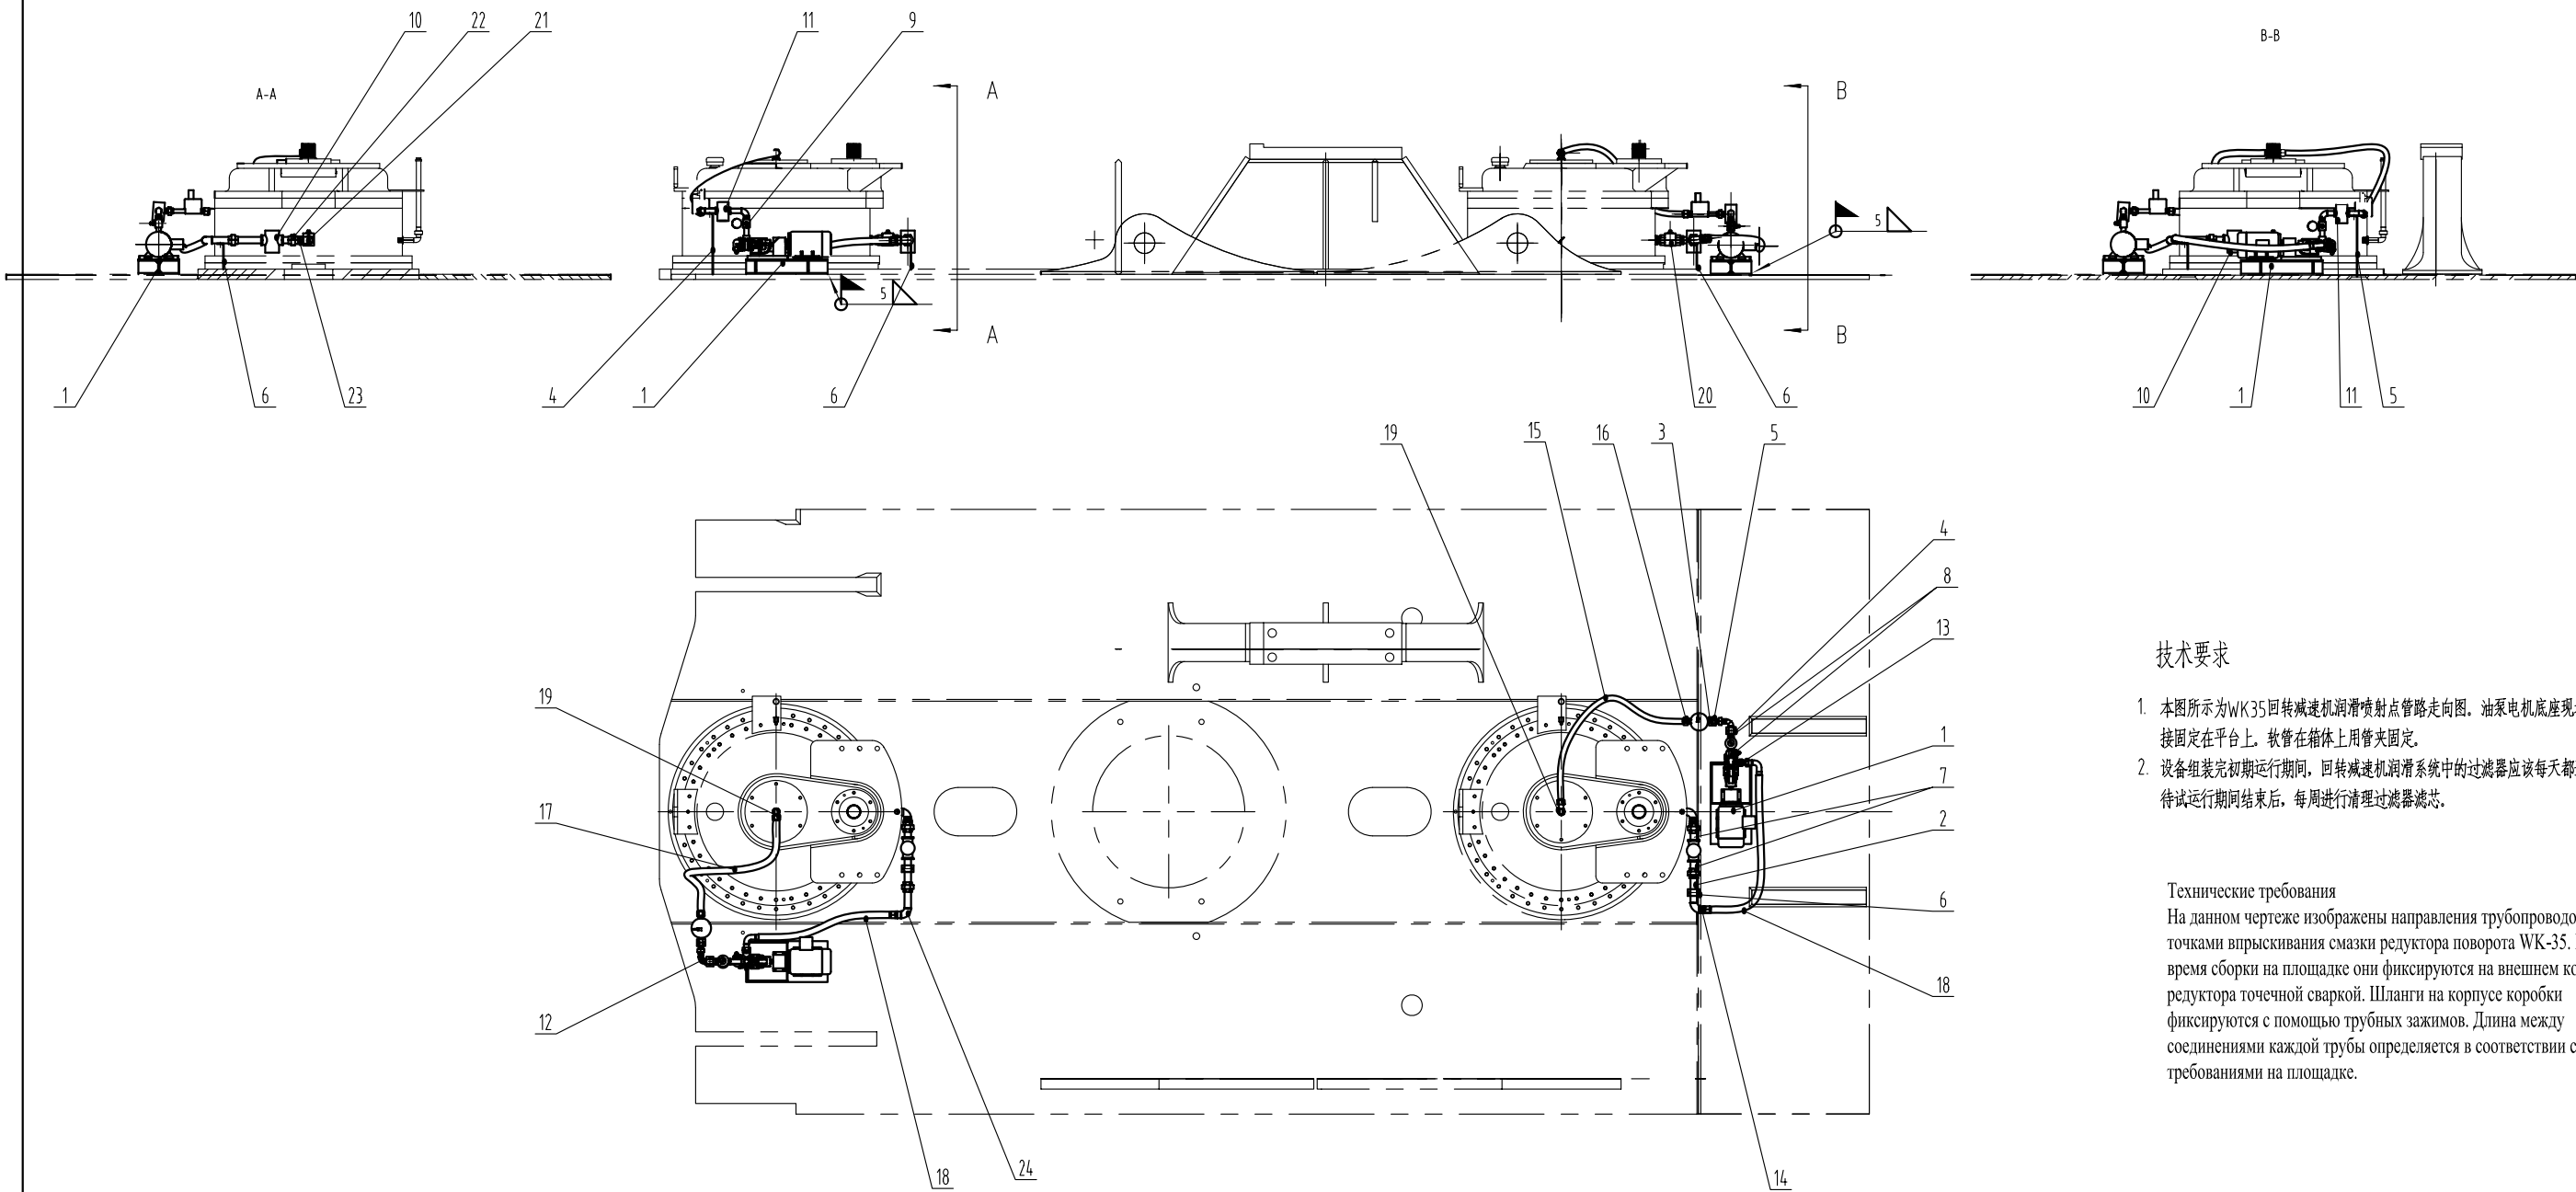

技术要求

1. 本图所示为WK35回转减速机润滑喷射点管路走向图。油泵电机底座现场装配时焊接固定在平台上。软管在箱体上用管夹固定。
2. 设备组装完初期运行期间，回转减速机润滑系统中的过滤器应该每天都进行清理，待试运行期间结束后，每周进行清理过滤器滤芯。

Технические требования

На данном чертеже изображены направления трубопроводов с точками впрыскивания смазки редуктора поворота WK-35. Во время сборки на площадке они фиксируются на внешнем корпусе редуктора точечной сваркой. Шланги на корпусе коробки фиксируются с помощью трубных зажимов. Длина между соединениями каждой трубы определяется в соответствии с требованиями на площадке.

P001000964-A				回转减速机润滑 СИСТЕМА СМАЗКИ РЕДУКТОРА ПОВОРОТА	K1838.93.00SH			
设 计	郭世英	工艺审查	袁运星					
校 核	卢安卿							
审 查	吕晓林	标准审查	白焱		重 量	217.36	比 例	1:50
主任设计		主管主任		通用技术条件 JB/T 5000	共 3 张		第 2 张	
所 长					 太重技术中心			
日 期	20161209							